NORTHGATE REGIONAL COUNCIL

KESTREL ROAD UPGRADE


STAGE 2

BETWEEN MARLOW STREET AND IRONBARK AVENUE

DESIGN PACKAGE RW01

ROADWORKS

100% DETAILED DESIGN

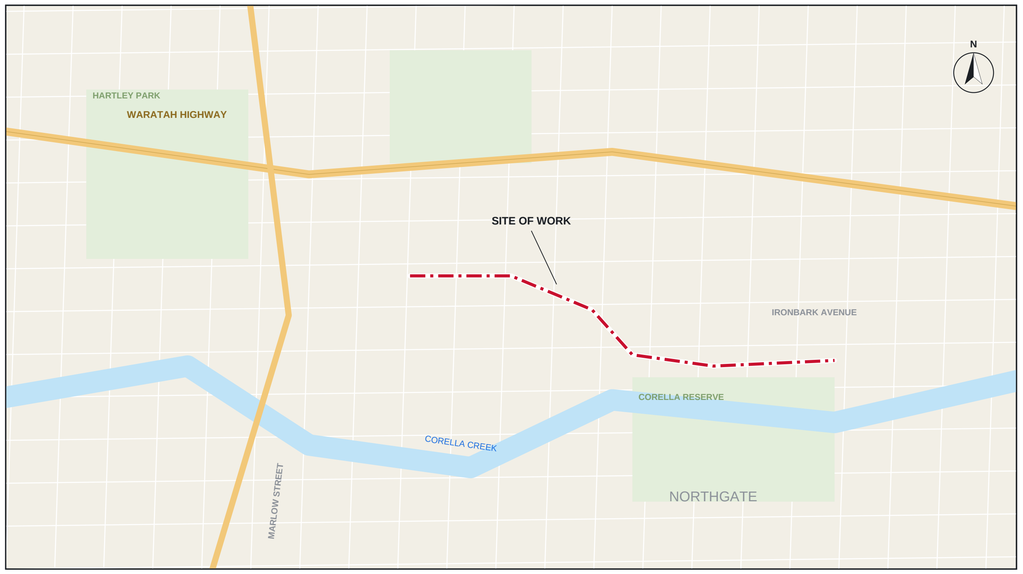

LOCALITY PLAN

NOT TO SCALE

DRAWING COLOUR CODED - PRINT ALL COPIES IN COLOUR

UNOFFICIAL

FOR REVIEW AND COMMENT

CLIENT

NORTHGATE
REGIONAL COUNCIL
Infrastructure Delivery | Roads & Drainage

PROJECT

PROJECT No 25-0412

KESTREL ROAD UPGRADE

STAGE 2

Marlow Street to Ironbark Avenue
Northgate NSW 2217

DESIGN PACKAGE RW01 | ROADWORKS

PREPARED BY

MERIDIAN
CIVIL CONSULTING

Level 9, 140 Harbour Street, Sydney NSW 2000
Tel: +61 2 5550 0142
meridiancivil.example

DRAWING TITLE

COVER SHEET

AND LOCALITY PLAN

SHEET 1 OF 1

DRAWING No.

KRU2-MCC-0412-RW-DRG-000001

REV	STATUS / SUITABILITY	ISSUE DATE
C	S3 FOR REVIEW AND COMMENT Not for construction	30.10.26

EDMS No	SHEET SIZE	SCALE @ A1
DS2026/01877	A1	NTS

REV	DESCRIPTION	BY	CHK	APP	DATE
A	50% DETAILED DESIGN	AN	SI	TM	28.05.26
B	80% DETAILED DESIGN	AN	SI	TM	14.08.26
C	100% DETAILED DESIGN	AN	SI	TM	30.10.26

ROLE	NAME	INITIALS	DATE
DRAWN	AMINA NGUYEN	AN	30.10.26
DESIGNED	RAFAEL OKAFOR	RO	30.10.26
DRAWING CHECK	LENA HARTMANN	LH	30.10.26
DESIGN CHECK	SANJAY IYER	SI	30.10.26
PROJECT MANAGER	DEIRDRE KOWALSKI	DK	30.10.26
APPROVED	TOBY McALLISTER	TM	30.10.26

COORDINATE SYSTEM	HEIGHT DATUM
GDA2020 / MGA ZONE 56	AHD71
DISCIPLINE	DESIGN LOT CODE
ROADWORKS	LOT-03
CONTRACT No	BRIDGE / ASSET No
NRC-C-2026-014	N/A
REFERENCES	AMENDMENT No
KRU2-MCC-0412-GN-M2D-000001	AMD-0006

SCAN FOR LATEST REV

COPYRIGHT AND DISCLAIMER

This drawing and the related information have been prepared by, or at the request of, Northgate Regional Council for a specific purpose and may not be used for any purpose other than the purpose intended. Northgate Regional Council does not provide any warranties and accepts no liability arising out of the use of this drawing for any other purpose. This drawing is protected by copyright and no part may be reproduced in any form without the express written permission of Northgate Regional Council.

DRAWING COLOUR CODED - PRINT ALL COPIES IN COLOUR

FILE NAME	PLOT DATE & TIME
KRU2-MCC-0412-RW-DRG-000001.dwg	30/10/2026 4:12:05 PM

DRAWING INDEX

DRAWING NUMBER	DISCIPLINE	DRAWING TITLE	SHEET	SCALE	REV
KRU2-MCC-0412-RW-DRG-000001	ROADWORKS	COVER SHEET AND LOCALITY PLAN	SHEET 1	NTS	C
KRU2-MCC-0412-RW-DRG-000002	ROADWORKS	DRAWING INDEX	SHEET 1	NTS	C
KRU2-MCC-0412-RW-DRG-000011	ROADWORKS	GENERAL LEGEND AND NOTES	SHEET 1	NTS	C
KRU2-MCC-0412-RW-DRG-000021	ROADWORKS	TYPICAL SECTIONS	SHEET 1	1:50	C
KRU2-MCC-0412-RW-DRG-000022	ROADWORKS	TYPICAL SECTIONS	SHEET 2	AS SHOWN	C
KRU2-MCC-0412-RW-DRG-000031	ROADWORKS	ALIGNMENT CONTROL PLAN	SHEET 1	1:500	C
KRU2-MCC-0412-RW-DRG-000032	ROADWORKS	ALIGNMENT CONTROL PLAN	SHEET 2	1:500	C
KRU2-MCC-0412-RW-DRG-000033	ROADWORKS	ALIGNMENT CONTROL PLAN	SHEET 3	1:500	C
KRU2-MCC-0412-RW-DRG-000034	ROADWORKS	ALIGNMENT CONTROL PLAN	SHEET 4	1:500	C
KRU2-MCC-0412-RW-DRG-000056	ROADWORKS	MAIN CONTROL LINES SETOUT TABLES	SHEET 1	NTS	C
KRU2-MCC-0412-RW-DRG-000201	ROADWORKS	LONGITUDINAL SECTIONS CONTROL LINE MC00	SHEET 1	AS SHOWN	C
KRU2-MCC-0412-RW-DRG-000202	ROADWORKS	LONGITUDINAL SECTIONS CONTROL LINE MC00	SHEET 2	AS SHOWN	C
KRU2-MCC-0412-RW-DRG-000203	ROADWORKS	LONGITUDINAL SECTIONS CONTROL LINE MC00	SHEET 3	AS SHOWN	C
KRU2-MCC-0412-RW-DRG-000204	ROADWORKS	LONGITUDINAL SECTIONS CONTROL LINE MC00	SHEET 4	AS SHOWN	C
KRU2-MCC-0412-RW-DRG-000221	ROADWORKS	LONGITUDINAL SECTIONS CONTROL LINE MC01 AND DRAINAGE LINE D01	SHEET 1	AS SHOWN	C
KRU2-MCC-0412-RW-DRG-000301	ROADWORKS	CROSS SECTIONS CONTROL LINE MC00	SHEET 1	1:100	C
KRU2-MCC-0412-RW-DRG-000302	ROADWORKS	CROSS SECTIONS CONTROL LINE MC00	SHEET 2	1:100	C
KRU2-MCC-0412-RW-DRG-000303	ROADWORKS	CROSS SECTIONS CONTROL LINE MC00	SHEET 3	1:100	C
KRU2-MCC-0412-RW-DRG-000304	ROADWORKS	CROSS SECTIONS CONTROL LINE MC00	SHEET 4	1:100	C
KRU2-MCC-0412-RW-DRG-000305	ROADWORKS	CROSS SECTIONS CONTROL LINE MC00	SHEET 5	1:100	C

STATUS KEY

S0 DRAFT
S2 FOR INFORMATION
S3 FOR REVIEW AND COMMENT
S4 FOR APPROVAL
S6 ISSUED FOR CONSTRUCTION

DRAWING NUMBER FORMAT

KRU2-MCC-0412-RW-DRG-000000

KRU2 = KESTREL ROAD UPGRADE STAGE 2 | MCC = MERIDIAN CIVIL CONSULTING
0412 = PROJECT No | RW = ROADWORKS | DRG = DRAWING
SIX-DIGIT SERIES: 0000xx GENERAL / 0000xx TYPICALS AND PLANS / 0002xx LONG SECTIONS / 0003xx CROSS SECTIONS

CLIENT

NORTHGATE
REGIONAL COUNCIL
Infrastructure Delivery | Roads & Drainage

PROJECT

PROJECT No 25-0412

KESTREL ROAD UPGRADE

STAGE 2

Marlow Street to Ironbark Avenue
Northgate NSW 2217

DESIGN PACKAGE RW01 | ROADWORKS

PREPARED BY

MERIDIAN
CIVIL CONSULTING

Level 9, 140 Harbour Street, Sydney NSW 2000
Tel: +61 2 5550 0142
meridiancivil.example

DRAWING TITLE

DRAWING INDEX

ROADWORKS

SHEET 1 OF 1

DRAWING No.

KRU2-MCC-0412-RW-DRG-000002

REV	STATUS / SUITABILITY	ISSUE DATE
C	S3 FOR REVIEW AND COMMENT Not for construction	30.10.26

EDMS No	SHEET SIZE	SCALE @ A1
DS2026/01877	A1	NTS

REV	DESCRIPTION	BY	CHK	APP	DATE
A	50% DETAILED DESIGN	AN	SI	TM	28.05.26
B	80% DETAILED DESIGN	AN	SI	TM	14.08.26
C	100% DETAILED DESIGN	AN	SI	TM	30.10.26

ROLE	NAME	INITIALS	DATE
DRAWN	AMINA NGUYEN	AN	30.10.26
DESIGNED	RAFAEL OKAFOR	RO	30.10.26
DRAWING CHECK	LENA HARTMANN	LH	30.10.26
DESIGN CHECK	SANJAY IYER	SI	30.10.26
PROJECT MANAGER	DEIRDRE KOWALSKI	DK	30.10.26
APPROVED	TOBY McALLISTER	TM	30.10.26

COORDINATE SYSTEM	HEIGHT DATUM
GDA2020 / MGA ZONE 56	AHD71
DISCIPLINE	DESIGN LOT CODE
ROADWORKS	LOT-03
CONTRACT No	BRIDGE / ASSET No
NRC-C-2026-014	N/A
REFERENCES	AMENDMENT No
KRU2-MCC-0412-GN-M2D-000001	AMD-0006

SCAN FOR LATEST REV

COPYRIGHT AND DISCLAIMER

This drawing and the related information have been prepared by, or at the request of, Northgate Regional Council for a specific purpose and may not be used for any purpose other than the purpose intended. Northgate Regional Council does not provide any warranties and accepts no liability arising out of the use of this drawing for any other purpose. This drawing is protected by copyright and no part may be reproduced in any form without the express written permission of Northgate Regional Council.

DRAWING COLOUR CODED - PRINT ALL COPIES IN COLOUR

FILE NAME	PLOT DATE & TIME
KRU2-MCC-0412-RW-DRG-000002.dwg	30/10/2026 4:12:05 PM

GENERAL

- CADASTRAL BOUNDARY
- PROJECT BOUNDARY
- CONSTRUCTION BOUNDARY
- LIMIT OF WORKS
- EXISTING ROAD EDGE
- NEW ROAD DESIGN
- EXISTING PAVEMENT
- MCX — CONTROL LINE ALIGNMENT LABEL
- CONTROL LINE ALIGNMENT
- PROPOSED CHANNEL
- NEW CROSS DRAINAGE CULVERT

ROADWORKS

- NEW STREET LIGHTING
- SHARED PATH / FOOTPATH
- TYPE F BARRIER
- STEEL RAIL BARRIER
- PEDESTRIAN FENCE
- STORMWATER PIT

SURVEY LEGEND

- POWER POLE
- SEWER MANHOLE
- WATER HYDRANT
- TREE
- BUILDING
- SEWER
- WATER MAIN
- UNDERGROUND POWER
- TELECOMMUNICATIONS

GENERAL NOTES

1. REDUCED LEVELS ARE TO AUSTRALIAN HEIGHT DATUM (AHD71).
2. COORDINATE CONTROL IS ON MAP GRID OF AUSTRALIA (MGA ZONE 56, GDA2020).
3. ALL DIMENSIONS ARE IN METRES UNLESS NOTED OTHERWISE. PAVEMENT THICKNESSES ARE IN MILLIMETRES. ALL LEVELS, COORDINATES AND CHAINAGES ARE EXPRESSED IN METRES.
4. THIS DRAWING SET IS A FICTIONAL SAMPLE PREPARED TO DEMONSTRATE DOCUMENT CONTROL AND MARKUP WORKFLOWS. IT MUST NOT BE USED FOR CONSTRUCTION.
5. EXISTING SERVICES ARE SHOWN FROM SURVEY AND DIAL BEFORE YOU DIG RECORDS ONLY. THE CONTRACTOR SHALL CONFIRM POSITION AND DEPTH BY POTHOLING BEFORE EXCAVATION.
6. CONTROL LINE MC00 IS THE CROWN OF KESTREL ROAD. MC01 IS THE CROWN OF HARTLEY STREET. OFFSETS ARE POSITIVE TO THE RIGHT LOOKING UP CHAINAGE.
7. KERB AND GUTTER IS TYPE SM2 UNLESS NOTED. REFER TO TYPICAL SECTIONS FOR PAVEMENT COMPOSITION.
8. STORMWATER PIPES ARE CLASS 2 RCP WITH RUBBER RING JOINTS UNLESS NOTED.
9. ALL WORKS SHALL BE CARRIED OUT IN ACCORDANCE WITH THE COUNCIL ENGINEERING STANDARDS AND THE SPECIFICATION.

ABBREVIATIONS

AC	ASPHALTIC CONCRETE	**K&G**	KERB AND GUTTER
AHD	AUSTRALIAN HEIGHT DATUM	**MGA**	MAP GRID OF AUSTRALIA
BOK	BACK OF KERB	**RCBC**	REINFORCED CONCRETE BOX CULVERT
CH	CHAINAGE	**RCP**	REINFORCED CONCRETE PIPE
CL	CONTROL LINE / CENTRE LINE	**RL**	REDUCED LEVEL
DGB	DENSE GRADED BASE	**SEW**	SEWER
DGS	DENSE GRADED SUBBASE	**TC / CT**	TANGENT TO CURVE / CURVE TO TANGENT
EX	EXISTING	**TEL**	TELECOMMUNICATIONS
FL	FLOW LINE	**UGE**	UNDERGROUND ELECTRICAL
IL	INVERT LEVEL	**WM**	WATER MAIN

SHEET REVISION NOTES

REV A 50% DETAILED DESIGN - ISSUED FOR COUNCIL REVIEW
REV B 80% DETAILED DESIGN - SERVICES AND DRAINAGE ADDED
REV C 100% DETAILED DESIGN - CULVERT AND LEVELS UPDATED

CLIENT

NORTHGATE REGIONAL COUNCIL
Infrastructure Delivery | Roads & Drainage

PROJECT — PROJECT No 25-0412

KESTREL ROAD UPGRADE

STAGE 2

Marlow Street to Ironbark Avenue
Northgate NSW 2217

DESIGN PACKAGE RW01 | ROADWORKS

PREPARED BY

MERIDIAN
CIVIL CONSULTING

Level 9, 140 Harbour Street, Sydney NSW 2000
Tel: +61 2 5550 0142
meridiancivil.example

DRAWING TITLE

GENERAL LEGEND

AND NOTES

SHEET 1 OF 1

DRAWING No.

KRU2-MCC-0412-RW-DRG-000011

REV	STATUS / SUITABILITY	ISSUE DATE
C	S3 FOR REVIEW AND COMMENT Not for construction	30.10.26

EDMS No	SHEET SIZE	SCALE @ A1
DS2026/01877	A1	NTS

REV	DESCRIPTION	BY	CHK	APP	DATE
A	50% DETAILED DESIGN	AN	SI	TM	28.05.26
B	80% DETAILED DESIGN	AN	SI	TM	14.08.26
C	100% DETAILED DESIGN	AN	SI	TM	30.10.26

ROLE	NAME	INITIALS	DATE
DRAWN	AMINA NGUYEN	AN	30.10.26
DESIGNED	RAFAEL OKAFOR	RO	30.10.26
DRAWING CHECK	LENA HARTMANN	LH	30.10.26
DESIGN CHECK	SANJAY IYER	SI	30.10.26
PROJECT MANAGER	DEIRDRE KOWALSKI	DK	30.10.26
APPROVED	TOBY McALLISTER	TM	30.10.26

COORDINATE SYSTEM	HEIGHT DATUM
GDA2020 / MGA ZONE 56	AHD71
DISCIPLINE	DESIGN LOT CODE
ROADWORKS	LOT-03
CONTRACT No	BRIDGE / ASSET No
NRC-C-2026-014	N/A
REFERENCES	AMENDMENT No
KRU2-MCC-0412-GN-M2D-000001	AMD-0006


SCAN FOR LATEST REV

COPYRIGHT AND DISCLAIMER

This drawing and the related information have been prepared by, or at the request of, Northgate Regional Council for a specific purpose and may not be used for any purpose other than the purpose intended. Northgate Regional Council does not provide any warranties and accepts no liability arising out of the use of this drawing for any other purpose. This drawing is protected by copyright and no part may be reproduced in any form without the express written permission of Northgate Regional Council.

DRAWING COLOUR CODED - PRINT ALL COPIES IN COLOUR


FILE NAME	PLOT DATE & TIME
KRU2-MCC-0412-RW-DRG-000011.dwg	30/10/2026 4:12:05 PM

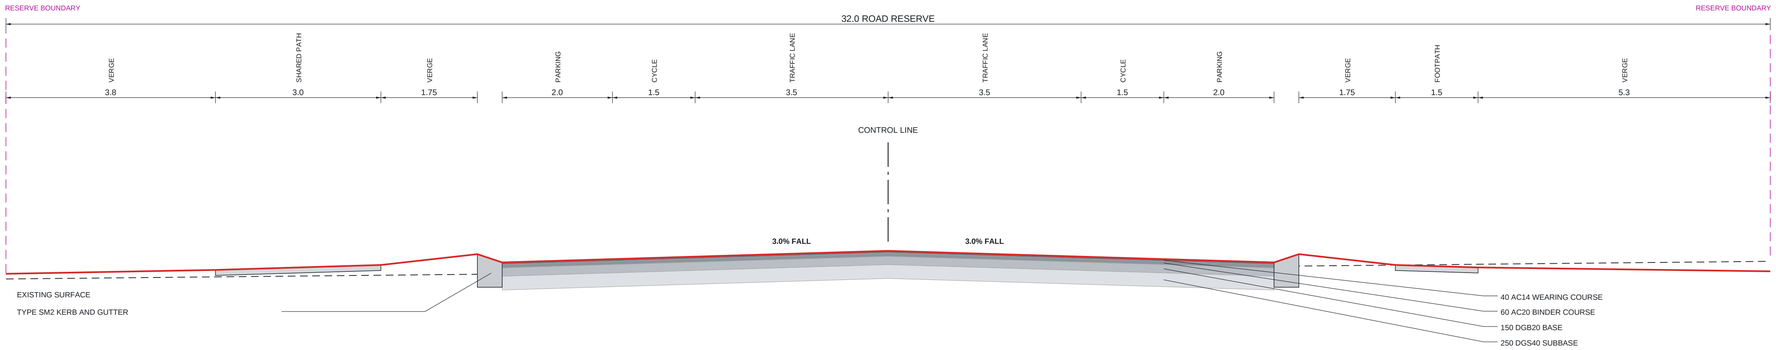

TYPICAL SECTION TS01 - KESTREL ROAD (MC00)

NORMAL CROWN - CH 0 TO CH 270 AND CH 840 TO CH 1040 SCALE 1:50

1. PAVEMENT TYPE P1 UNLESS NOTED. 2. KERB AND GUTTER TYPE SM2 BOTH SIDES.
3. STORMWATER DRAINAGE AT 8.6 m RIGHT, SERVICES IN VERGES AS SHOWN ON PLAN.

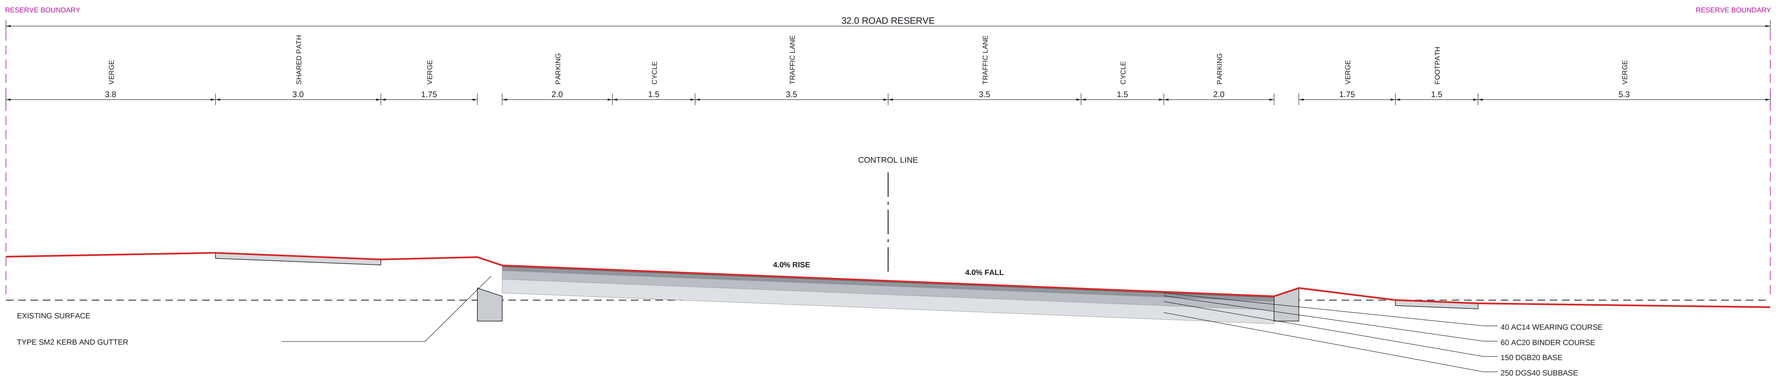

TYPICAL SECTION TS02 - KESTREL ROAD (MC00)

SUPERELEVATED - CH 340 TO CH 530 (RIGHT) AND CH 600 TO CH 790 (LEFT) SCALE 1:50

1. FULL SUPERELEVATION 4% SHOWN FOR THE RIGHT-HAND CURVE. REVERSE FOR THE LEFT-HAND CURVE.
2. TRANSITIONS PER THE CROSSFALL BAND ON THE LONGITUDINAL SECTIONS.

CLIENT

NORTHGATE REGIONAL COUNCIL
Infrastructure Delivery | Roads & Drainage

PROJECT

PROJECT No 25-0412

KESTREL ROAD UPGRADE

STAGE 2

Marlow Street to Ironbark Avenue
Northgate NSW 2217

DESIGN PACKAGE RW01 | ROADWORKS

PREPARED BY

MERIDIAN
CIVIL CONSULTING

Level 9, 140 Harbour Street, Sydney NSW 2000
Tel: +61 2 5550 0142
meridiancivil.example

DRAWING TITLE

TYPICAL SECTIONS

KESTREL ROAD (MC00)

SHEET 1 OF 2

DRAWING No.

KRU2-MCC-0412-RW-DRG-000021

REV	STATUS / SUITABILITY	ISSUE DATE
C	S3 FOR REVIEW AND COMMENT Not for construction	30.10.26

EDMS No	SHEET SIZE	SCALE @ A1
DS2026/01877	A1	1:50

REV	DESCRIPTION	BY	CHK	APP	DATE
A	50% DETAILED DESIGN	AN	SI	TM	28.05.26
B	80% DETAILED DESIGN	AN	SI	TM	14.08.26
C	100% DETAILED DESIGN	AN	SI	TM	30.10.26

ROLE	NAME	INITIALS	DATE
DRAWN	AMINA NGUYEN	AN	30.10.26
DESIGNED	RAFAEL OKAFOR	RO	30.10.26
DRAWING CHECK	LENA HARTMANN	LH	30.10.26
DESIGN CHECK	SANJAY IYER	SI	30.10.26
PROJECT MANAGER	DEIRDRE KOWALSKI	DK	30.10.26
APPROVED	TOBY McALLISTER	TM	30.10.26

COORDINATE SYSTEM	HEIGHT DATUM
GDA2020 / MGA ZONE 56	AHD71
DISCIPLINE	DESIGN LOT CODE
ROADWORKS	LOT-03
CONTRACT No	BRIDGE / ASSET No
NRC-C-2026-014	N/A
REFERENCES	AMENDMENT No
KRU2-MCC-0412-GN-M2D-000001	AMD-0006


SCAN FOR LATEST REV

COPYRIGHT AND DISCLAIMER

This drawing and the related information have been prepared by, or at the request of, Northgate Regional Council for a specific purpose and may not be used for any purpose other than the purpose intended. Northgate Regional Council does not provide any warranties and accepts no liability arising out of the use of this drawing for any other purpose. This drawing is protected by copyright and no part may be reproduced in any form without the express written permission of Northgate Regional Council.

DRAWING COLOUR CODED - PRINT ALL COPIES IN COLOUR

FILE NAME	PLOT DATE & TIME
KRU2-MCC-0412-RW-DRG-000021.dwg	30/10/2026 4:12:05 PM

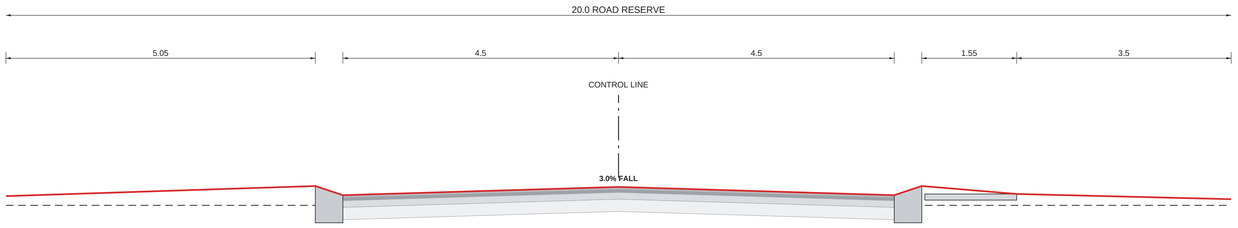

TYPICAL SECTION TS03 - HARTLEY STREET (MC01)

TWO-WAY, NO KERBSIDE PARKING SCALE 1:50


PAVEMENT COMPOSITION

TYPE	LOCATION	SURFACING	BASE	SUBBASE	TOTAL
P1	KESTREL ROAD	40 AC14 + 60 AC20	150 DGB20	250 DGS40	500
P2	HARTLEY STREET	40 AC10 + 50 AC14	150 DGB20	200 DGS40	440
P3	CULVERT APPROACH	40 AC14 + 60 AC20	200 CTB	250 DGS40	550
P4	SHARED PATH	100 PLAIN CONCRETE	100 DGB20	-	200
P5	FOOTPATH	75 PLAIN CONCRETE	75 DGB20	-	150

THICKNESSES IN mm. SUBGRADE DESIGN CBR 5%.


KERB AND GUTTER TYPE SM2

SCALE 1:10

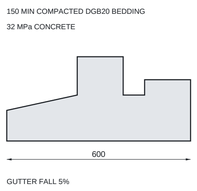


STORMWATER TRENCH DETAIL

SCALE 1:20

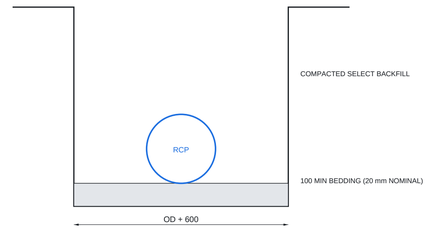


SHARED PATH DETAIL

SCALE 1:20

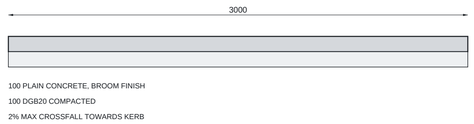

NEW CULVERT - TYPICAL SECTION

3/2400 x 1200 RCBC AT CH 914.82 SCALE 1:50

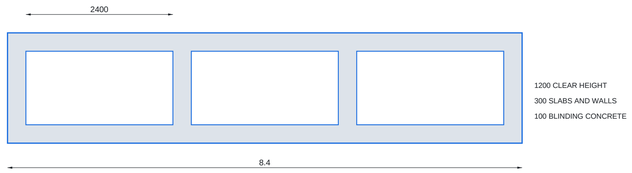

SERVICE ALLOCATIONS WITHIN RESERVE

SERVICE	OFFSET FROM CL	MIN COVER	OWNER
SEWER (SEW)	15.0 LEFT	1.2 m	COUNCIL
UNDERGROUND POWER (UGE)	13.4 LEFT	0.6 m	ENERGY NETWORK
WATER MAIN (WM)	12.4 RIGHT	0.75 m	COUNCIL
TELECOMMUNICATIONS (TEL)	13.6 RIGHT	0.6 m	CARRIER
STORMWATER D01	8.6 RIGHT	0.6 m	COUNCIL

CLIENT

NORTHGATE REGIONAL COUNCIL
Infrastructure Delivery | Roads & Drainage

PROJECT PROJECT No 25-0412

KESTREL ROAD UPGRADE

STAGE 2

Marlow Street to Ironbark Avenue
Northgate NSW 2217

DESIGN PACKAGE RW01 | ROADWORKS

PREPARED BY

MERIDIAN
CIVIL CONSULTING
Level 9, 140 Harbour Street, Sydney NSW 2000
Tel: +61 2 5550 0142
meridiancivil.example

DRAWING TITLE

TYPICAL SECTIONS

SIDE ROAD AND DETAILS

SHEET 2 OF 2

DRAWING No.

KRU2-MCC-0412-RW-DRG-000022

REV	STATUS / SUITABILITY	ISSUE DATE
C	**S3 FOR REVIEW AND COMMENT** — Not for construction	**30.10.26**

EDMS No	SHEET SIZE	SCALE @ A1
DS2026/01877	**A1**	**AS SHOWN**

REV	DESCRIPTION	BY	CHK	APP	DATE
A	50% DETAILED DESIGN	AN	SI	TM	28.05.26
B	80% DETAILED DESIGN	AN	SI	TM	14.08.26
C	100% DETAILED DESIGN	AN	SI	TM	30.10.26

ROLE	NAME	INITIALS	DATE
DRAWN	AMINA NGUYEN	AN	30.10.26
DESIGNED	RAFAEL OKAFOR	RO	30.10.26
DRAWING CHECK	LENA HARTMANN	LH	30.10.26
DESIGN CHECK	SANJAY IYER	SI	30.10.26
PROJECT MANAGER	DEIRDRE KOWALSKI	DK	30.10.26
APPROVED	TOBY McALLISTER	TM	30.10.26

COORDINATE SYSTEM	HEIGHT DATUM
GDA2020 / MGA ZONE 56	**AHD71**
DISCIPLINE	DESIGN LOT CODE
ROADWORKS	**LOT-03**
CONTRACT No	BRIDGE / ASSET No
NRC-C-2026-014	**N/A**
REFERENCES	AMENDMENT No
KRU2-MCC-0412-GN-M2D-000001	**AMD-0006**

SCAN FOR LATEST REV

COPYRIGHT AND DISCLAIMER

This drawing and the related information have been prepared by, or at the request of, Northgate Regional Council for a specific purpose and may not be used for any purpose other than the purpose intended. Northgate Regional Council does not provide any warranties and accepts no liability arising out of the use of this drawing for any other purpose. This drawing is protected by copyright and no part may be reproduced in any form without the express written permission of Northgate Regional Council.

DRAWING COLOUR CODED - PRINT ALL COPIES IN COLOUR

FILE NAME	PLOT DATE & TIME
KRU2-MCC-0412-RW-DRG-000022.dwg	30/10/2026 4:12:05 PM

N

LEGEND


- CADASTRAL BOUNDARY
- PROJECT BOUNDARY
- CONSTRUCTION BOUNDARY
- LIMIT OF WORKS
- EXISTING ROAD
- NEW ROAD DESIGN
- SHARED PATH / FOOTPATH
- CONTROL LINE ALIGNMENT
- CONTROL LINE ALIGNMENT LABEL (MCX)
- PROPOSED STORMWATER DRAINAGE
- NEW CROSS DRAINAGE CULVERT
- STREET LIGHT
- EXISTING SEWER (SEW)
- EXISTING WATER MAIN (WM)
- EXISTING UNDERGROUND POWER (UGE)
- EXISTING TELECOMMUNICATIONS (TEL)
- EXISTING TREE / BUILDING

NOTES

1. ALL DIMENSIONS ARE IN METRES UNLESS NOTED OTHERWISE.
2. FOR SETOUT SCHEDULES REFER TO DRG KRU2-MCC-0412-RW-DRG-000056.

KEY PLAN

NOT TO SCALE

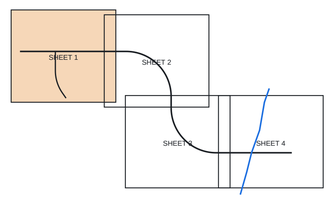

TO MARLOW STREET

START OF WORKS CH 0.000

MC00

SEW

UGE

KESTREL ROAD

WM

MC01

HARTLEY STREET

CH 130.000

HARTLEY STREET (EXISTING)
LIMIT OF WORKS CH 153.304

MATCH LINE CH 280.000
ADJOINS DRG KRU2-MCC-0412-RW-DRG-000032

0 10 20 40m
SCALE 1:500 @A1

CLIENT

NORTHGATE
REGIONAL COUNCIL
Infrastructure Delivery | Roads & Drainage

PROJECT

PROJECT No 25-0412

KESTREL ROAD UPGRADE

STAGE 2

Marlow Street to Ironbark Avenue
Northgate NSW 2217

DESIGN PACKAGE RW01 | ROADWORKS

PREPARED BY

MERIDIAN
CIVIL CONSULTING

Level 9, 140 Harbour Street, Sydney NSW 2000
Tel: +61 2 5550 0142
meridiancivil.example

DRAWING TITLE

ALIGNMENT CONTROL PLAN

CH 0 TO CH 280

SHEET 1 OF 4

DRAWING No.

KRU2-MCC-0412-RW-DRG-000031

REV	STATUS / SUITABILITY	ISSUE DATE
C	S3 FOR REVIEW AND COMMENT Not for construction	30.10.26

EDMS No	SHEET SIZE	SCALE @ A1
DS2026/01877	A1	1:500

REV	DESCRIPTION	BY	CHK	APP	DATE
A	50% DETAILED DESIGN	AN	SI	TM	28.05.26
B	80% DETAILED DESIGN	AN	SI	TM	14.08.26
C	100% DETAILED DESIGN	AN	SI	TM	30.10.26

ROLE	NAME	INITIALS	DATE
DRAWN	AMINA NGUYEN	AN	30.10.26
DESIGNED	RAFAEL OKAFOR	RO	30.10.26
DRAWING CHECK	LENA HARTMANN	LH	30.10.26
DESIGN CHECK	SANJAY IYER	SI	30.10.26
PROJECT MANAGER	DEIRDRE KOWALSKI	DK	30.10.26
APPROVED	TOBY McALLISTER	TM	30.10.26

COORDINATE SYSTEM	HEIGHT DATUM
GDA2020 / MGA ZONE 56	AHD71
DISCIPLINE	DESIGN LOT CODE
ROADWORKS	LOT-03
CONTRACT No	BRIDGE / ASSET No
NRC-C-2026-014	N/A
REFERENCES	AMENDMENT No
KRU2-MCC-0412-GN-M2D-000001	AMD-0006


SCAN FOR LATEST REV

COPYRIGHT AND DISCLAIMER

This drawing and the related information have been prepared by, or at the request of, Northgate Regional Council for a specific purpose and may not be used for any purpose other than the purpose intended. Northgate Regional Council does not provide any warranties and accepts no liability arising out of the use of this drawing for any other purpose. This drawing is protected by copyright and no part may be reproduced in any form without the express written permission of Northgate Regional Council.

DRAWING COLOUR CODED - PRINT ALL COPIES IN COLOUR

FILE NAME	PLOT DATE & TIME
KRU2-MCC-0412-RW-DRG-000031.dwg	30/10/2026 4:12:05 PM

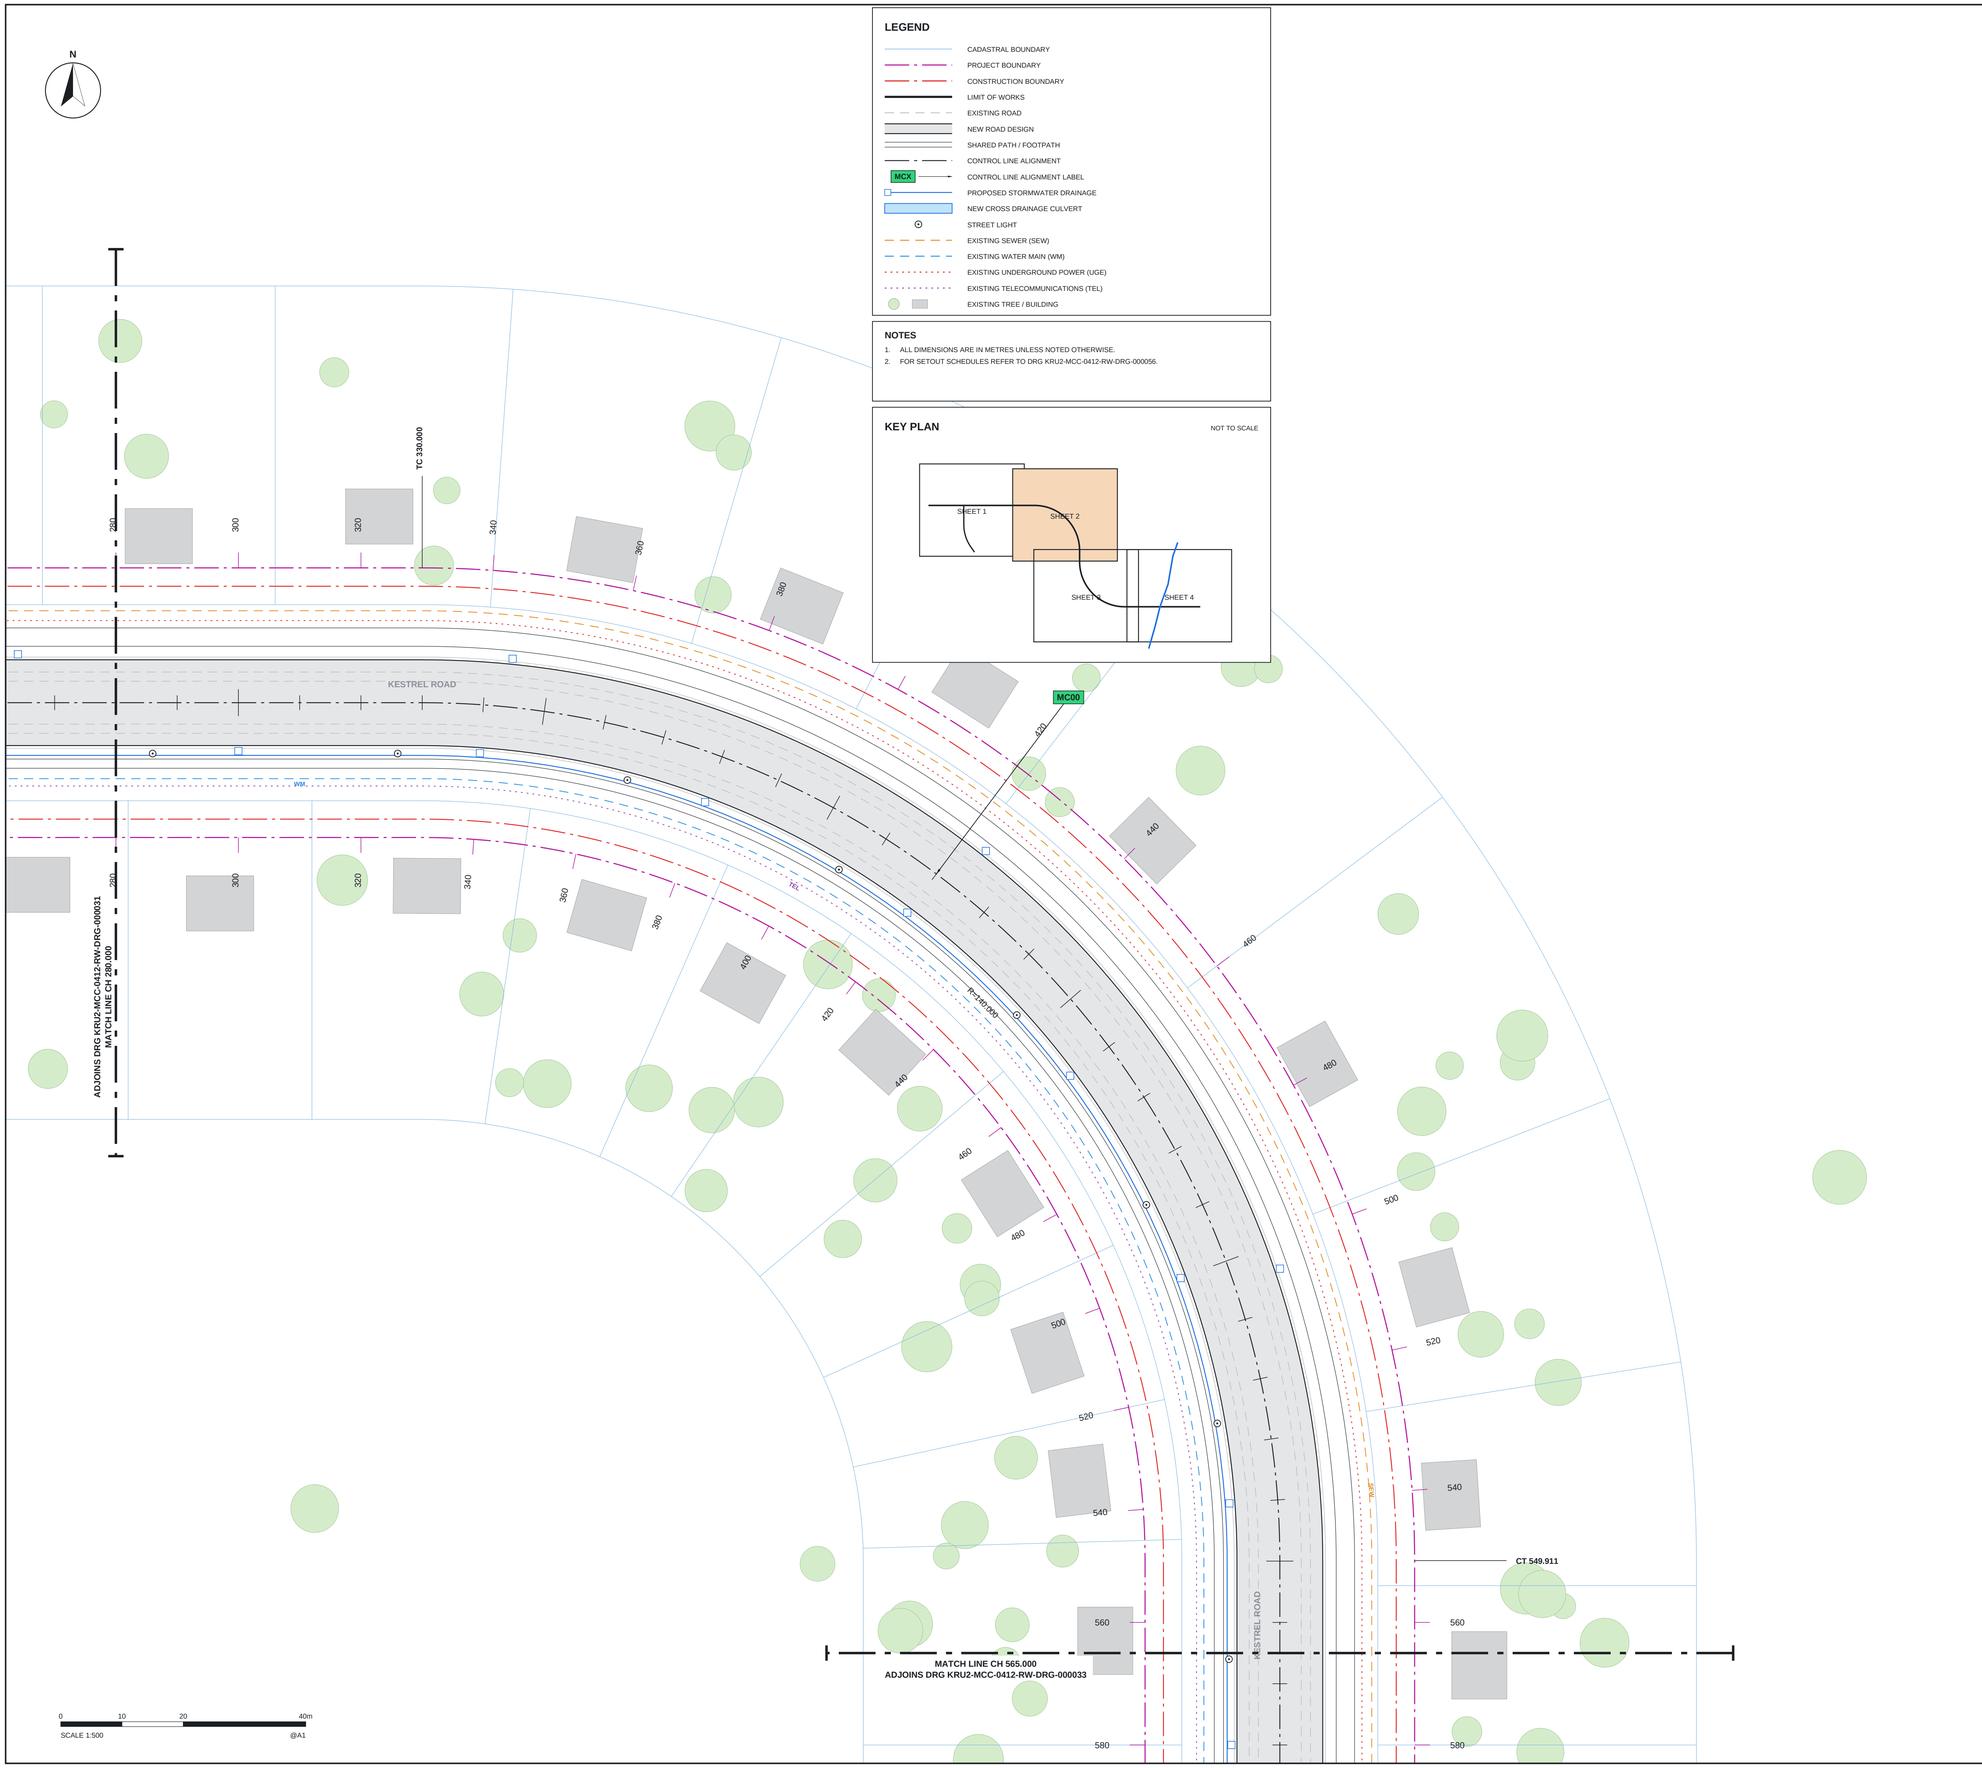

CLIENT

NORTHGATE
REGIONAL COUNCIL
Infrastructure Delivery | Roads & Drainage

PROJECT

PROJECT No 25-0412

KESTREL ROAD UPGRADE

STAGE 2

Marlow Street to Ironbark Avenue
Northgate NSW 2217

DESIGN PACKAGE RW01 | ROADWORKS

PREPARED BY

MERIDIAN
CIVIL CONSULTING

Level 9, 140 Harbour Street, Sydney NSW 2000
Tel: +61 2 5550 0142
meridiancivil.example

DRAWING TITLE

ALIGNMENT CONTROL PLAN

CH 280 TO CH 565

SHEET 2 OF 4

DRAWING No.

KRU2-MCC-0412-RW-DRG-000032

REV	STATUS / SUITABILITY	ISSUE DATE
C	S3 FOR REVIEW AND COMMENT Not for construction	30.10.26

EDMS No	SHEET SIZE	SCALE @ A1
DS2026/01877	A1	1:500

REV	DESCRIPTION	BY	CHK	APP	DATE
A	50% DETAILED DESIGN	AN	SI	TM	28.05.26
B	80% DETAILED DESIGN	AN	SI	TM	14.08.26
C	100% DETAILED DESIGN	AN	SI	TM	30.10.26

ROLE	NAME	INITIALS	DATE
DRAWN	AMINA NGUYEN	AN	30.10.26
DESIGNED	RAFAEL OKAFOR	RO	30.10.26
DRAWING CHECK	LENA HARTMANN	LH	30.10.26
DESIGN CHECK	SANJAY IYER	SI	30.10.26
PROJECT MANAGER	DEIRDRE KOWALSKI	DK	30.10.26
APPROVED	TOBY McALLISTER	TM	30.10.26

COORDINATE SYSTEM	HEIGHT DATUM
GDA2020 / MGA ZONE 56	AHD71

DISCIPLINE	DESIGN LOT CODE
ROADWORKS	LOT-03

CONTRACT No	BRIDGE / ASSET No
NRC-C-2026-014	N/A

REFERENCES	AMENDMENT No
KRU2-MCC-0412-GN-M2D-000001	AMD-0006


COPYRIGHT AND DISCLAIMER

This drawing and the related information have been prepared by, or at the request of, Northgate Regional Council for a specific purpose and may not be used for any purpose other than the purpose intended. Northgate Regional Council does not provide any warranties and accepts no liability arising out of the use of this drawing for any other purpose. This drawing is protected by copyright and no part may be reproduced in any form without the express written permission of Northgate Regional Council.

SCAN FOR LATEST REV

DRAWING COLOUR CODED - PRINT ALL COPIES IN COLOUR

FILE NAME	PLOT DATE & TIME
KRU2-MCC-0412-RW-DRG-000032.dwg	30/10/2026 4:12:05 PM

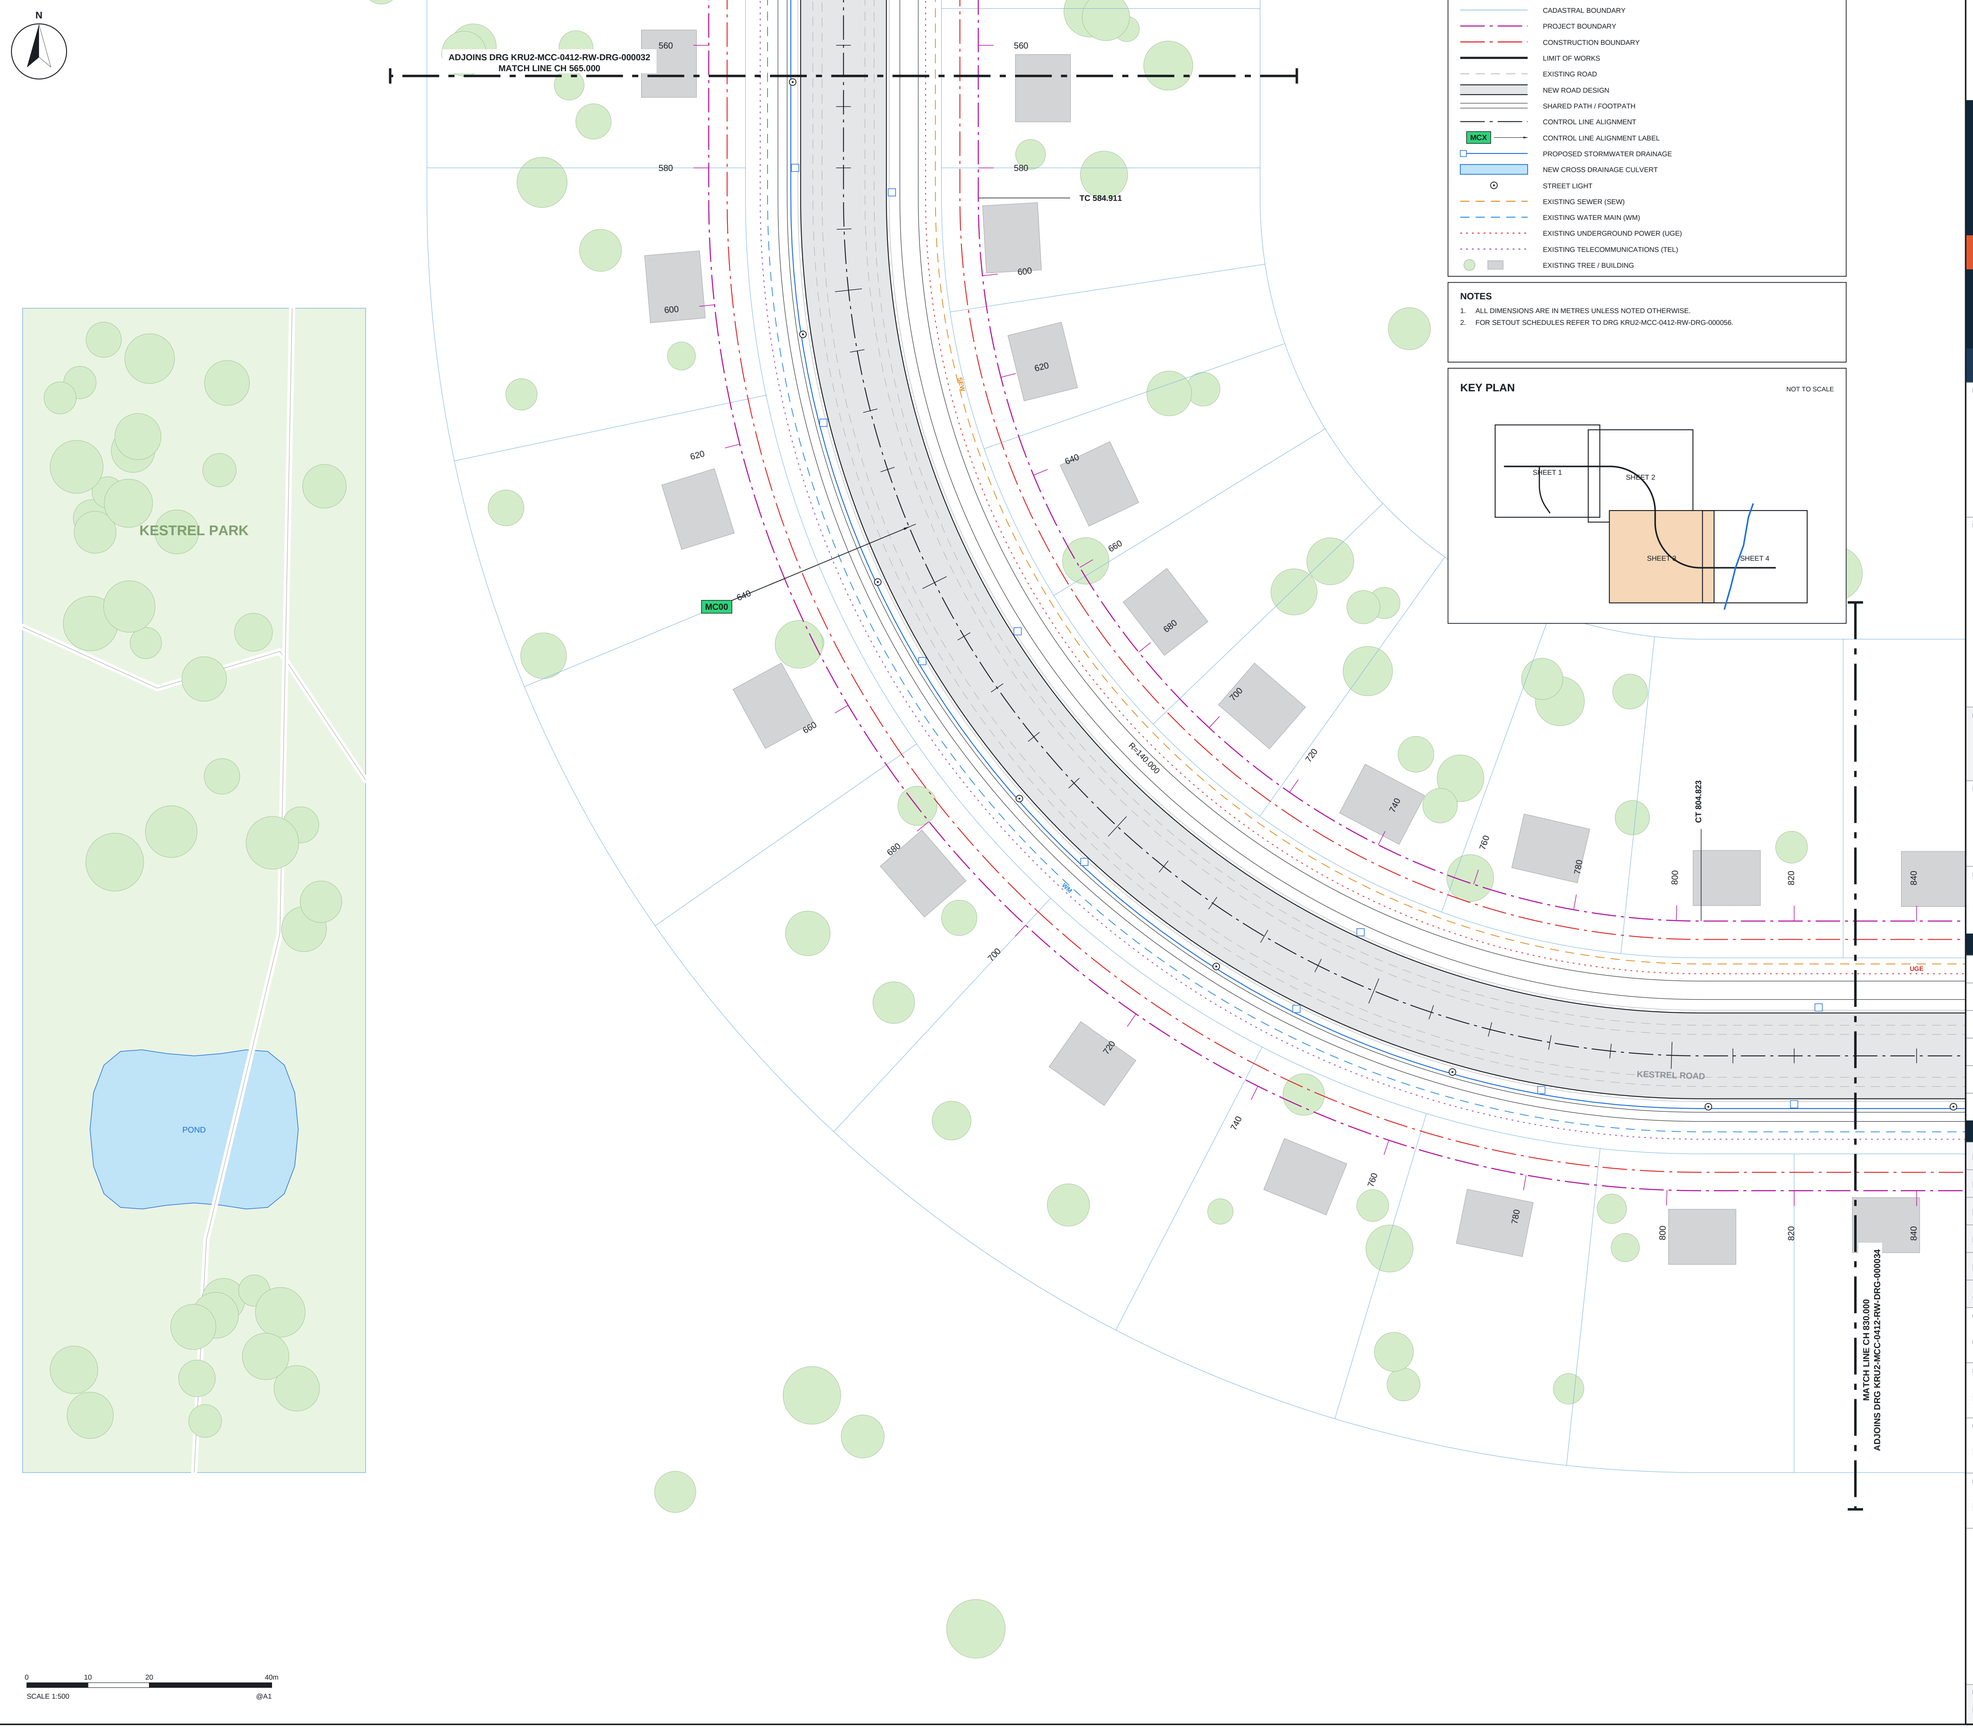

LEGEND

- CADASTRAL BOUNDARY
- PROJECT BOUNDARY
- CONSTRUCTION BOUNDARY
- LIMIT OF WORKS
- EXISTING ROAD
- NEW ROAD DESIGN
- SHARED PATH / FOOTPATH
- CONTROL LINE ALIGNMENT
- CONTROL LINE ALIGNMENT LABEL (MCX)
- PROPOSED STORMWATER DRAINAGE
- NEW CROSS DRAINAGE CULVERT
- STREET LIGHT
- EXISTING SEWER (SEW)
- EXISTING WATER MAIN (WM)
- EXISTING UNDERGROUND POWER (UGE)
- EXISTING TELECOMMUNICATIONS (TEL)
- EXISTING TREE / BUILDING

NOTES

1. ALL DIMENSIONS ARE IN METRES UNLESS NOTED OTHERWISE.
2. FOR SETOUT SCHEDULES REFER TO DRG KRU2-MCC-0412-RW-DRG-000056.

KEY PLAN

NOT TO SCALE

CLIENT

NORTHGATE REGIONAL COUNCIL
Infrastructure Delivery | Roads & Drainage

PROJECT

PROJECT No 25-0412

KESTREL ROAD UPGRADE

STAGE 2

Marlow Street to Ironbark Avenue
Northgate NSW 2217

DESIGN PACKAGE RW01 | ROADWORKS

PREPARED BY

MERIDIAN
CIVIL CONSULTING

Level 9, 140 Harbour Street, Sydney NSW 2000
Tel: +61 2 5550 0142
meridiancivil.example

DRAWING TITLE

ALIGNMENT CONTROL PLAN

CH 565 TO CH 830

SHEET 3 OF 4

DRAWING No.

KRU2-MCC-0412-RW-DRG-000033

REV	STATUS / SUITABILITY	ISSUE DATE
C	S3 FOR REVIEW AND COMMENT Not for construction	30.10.26

EDMS No	SHEET SIZE	SCALE @ A1
DS2026/01877	A1	1:500

REV	DESCRIPTION	BY	CHK	APP	DATE
A	50% DETAILED DESIGN	AN	SI	TM	28.05.26
B	80% DETAILED DESIGN	AN	SI	TM	14.08.26
C	100% DETAILED DESIGN	AN	SI	TM	30.10.26

ROLE	NAME	INITIALS	DATE
DRAWN	AMINA NGUYEN	AN	30.10.26
DESIGNED	RAFAEL OKAFOR	RO	30.10.26
DRAWING CHECK	LENA HARTMANN	LH	30.10.26
DESIGN CHECK	SANJAY IYER	SI	30.10.26
PROJECT MANAGER	DEIRDRE KOWALSKI	DK	30.10.26
APPROVED	TOBY McALLISTER	TM	30.10.26

COORDINATE SYSTEM	HEIGHT DATUM
GDA2020 / MGA ZONE 56	AHD71
DISCIPLINE	DESIGN LOT CODE
ROADWORKS	LOT-03
CONTRACT No	BRIDGE / ASSET No
NRC-C-2026-014	N/A
REFERENCES	AMENDMENT No
KRU2-MCC-0412-GN-M2D-000001	AMD-0006


COPYRIGHT AND DISCLAIMER

This drawing and the related information have been prepared by, or at the request of, Northgate Regional Council for a specific purpose and may not be used for any purpose other than the purpose intended. Northgate Regional Council does not provide any warranties and accepts no liability arising out of the use of this drawing for any other purpose. This drawing is protected by copyright and no part may be reproduced in any form without the express written permission of Northgate Regional Council.

SCAN FOR LATEST REV

DRAWING COLOUR CODED - PRINT ALL COPIES IN COLOUR

FILE NAME	PLOT DATE & TIME
KRU2-MCC-0412-RW-DRG-000033.dwg	30/10/2026 4:12:05 PM

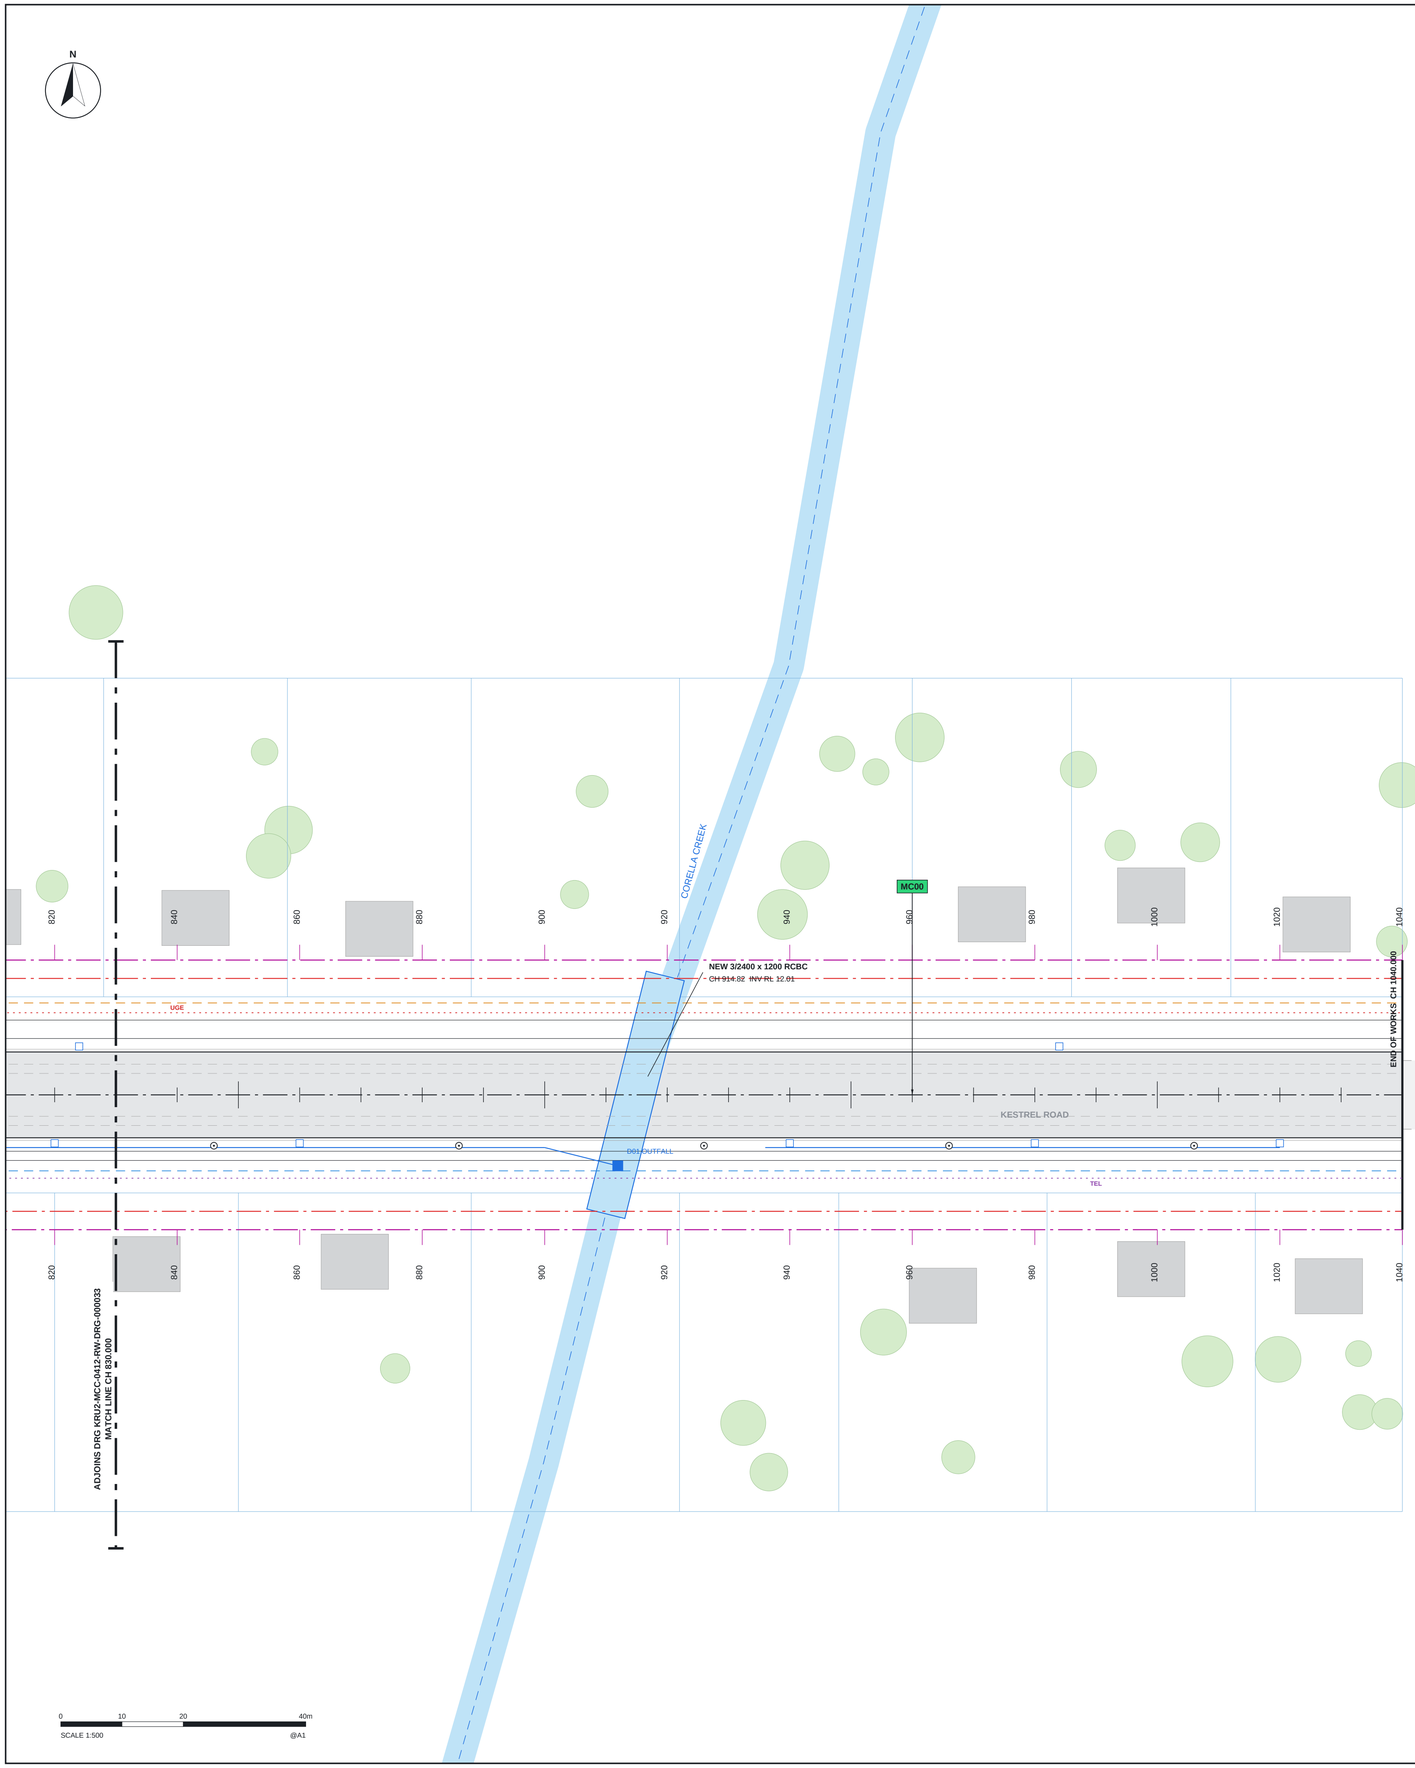

LEGEND


- CADASTRAL BOUNDARY
- PROJECT BOUNDARY
- CONSTRUCTION BOUNDARY
- LIMIT OF WORKS
- EXISTING ROAD
- NEW ROAD DESIGN
- SHARED PATH / FOOTPATH
- CONTROL LINE ALIGNMENT
- CONTROL LINE ALIGNMENT LABEL (MCX)
- PROPOSED STORMWATER DRAINAGE
- NEW CROSS DRAINAGE CULVERT
- STREET LIGHT
- EXISTING SEWER (SEW)
- EXISTING WATER MAIN (WM)
- EXISTING UNDERGROUND POWER (UGE)
- EXISTING TELECOMMUNICATIONS (TEL)
- EXISTING TREE / BUILDING

NOTES

1. ALL DIMENSIONS ARE IN METRES UNLESS NOTED OTHERWISE.
2. FOR SETOUT SCHEDULES REFER TO DRG KRU2-MCC-0412-RW-DRG-000056.

KEY PLAN

NOT TO SCALE

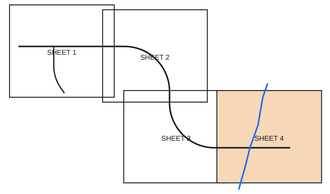

CLIENT

NORTHGATE
REGIONAL COUNCIL
Infrastructure Delivery | Roads & Drainage

PROJECT

PROJECT No 25-0412

KESTREL ROAD UPGRADE

STAGE 2

Marlow Street to Ironbark Avenue
Northgate NSW 2217

DESIGN PACKAGE RW01 | ROADWORKS

PREPARED BY

MERIDIAN
CIVIL CONSULTING

Level 9, 140 Harbour Street, Sydney NSW 2000
Tel: +61 2 5550 0142
meridiancivil.example

DRAWING TITLE

ALIGNMENT CONTROL PLAN

CH 830 TO CH 1040

SHEET 4 OF 4

DRAWING No.

KRU2-MCC-0412-RW-DRG-000034

REV	STATUS / SUITABILITY	ISSUE DATE
C	S3 FOR REVIEW AND COMMENT Not for construction	30.10.26

EDMS No	SHEET SIZE	SCALE @ A1
DS2026/01877	A1	1:500

REV	DESCRIPTION	BY	CHK	APP	DATE
A	50% DETAILED DESIGN	AN	SI	TM	28.05.26
B	80% DETAILED DESIGN	AN	SI	TM	14.08.26
C	100% DETAILED DESIGN	AN	SI	TM	30.10.26

ROLE	NAME	INITIALS	DATE
DRAWN	AMINA NGUYEN	AN	30.10.26
DESIGNED	RAFAEL OKAFOR	RO	30.10.26
DRAWING CHECK	LENA HARTMANN	LH	30.10.26
DESIGN CHECK	SANJAY IYER	SI	30.10.26
PROJECT MANAGER	DEIRDRE KOWALSKI	DK	30.10.26
APPROVED	TOBY McALLISTER	TM	30.10.26

COORDINATE SYSTEM	HEIGHT DATUM
GDA2020 / MGA ZONE 56	AHD71
DISCIPLINE	DESIGN LOT CODE
ROADWORKS	LOT-03
CONTRACT No	BRIDGE / ASSET No
NRC-C-2026-014	N/A
REFERENCES	AMENDMENT No
KRU2-MCC-0412-GN-M2D-000001	AMD-0006

COPYRIGHT AND DISCLAIMER

This drawing and the related information have been prepared by, or at the request of, Northgate Regional Council for a specific purpose and may not be used for any purpose other than the purpose intended. Northgate Regional Council does not provide any warranties and accepts no liability arising out of the use of this drawing for any other purpose. This drawing is protected by copyright and no part may be reproduced in any form without the express written permission of Northgate Regional Council.

SCAN FOR LATEST REV

DRAWING COLOUR CODED - PRINT ALL COPIES IN COLOUR

FILE NAME	PLOT DATE & TIME
KRU2-MCC-0412-RW-DRG-000034.dwg	30/10/2026 4:12:05 PM

MAIN CONTROL LINES SETOUT TABLES

CONTROL LINE MC00 - HORIZONTAL ALIGNMENT

PT	CHAINAGE	EASTING	NORTHING	BEARING	ELEMENT	RADIUS	LENGTH
START	0.000	318310.000	6247345.000	90°00'00"	STRAIGHT	-	330.000
TC	330.000	318640.000	6247345.000	90°00'00"	RIGHT CURVE	140.000	219.911
CT	549.911	318780.000	6247205.000	180°00'00"	STRAIGHT	-	35.000
TC	584.911	318780.000	6247170.000	180°00'00"	LEFT CURVE	140.000	219.911
CT	804.823	318920.000	6247030.000	90°00'00"	STRAIGHT	-	235.177
END	1040.000	319155.177	6247030.000	90°00'00"	-	-	-

CONTROL LINE MC01 - HORIZONTAL ALIGNMENT

PT	CHAINAGE	EASTING	NORTHING	BEARING	ELEMENT	RADIUS	LENGTH
START	0.000	318420.000	6247345.000	180°00'00"	STRAIGHT	-	60.000
TC	60.000	318420.000	6247285.000	180°00'00"	LEFT CURVE	120.000	73.304
CT	133.304	318441.702	6247216.171	145°00'00"	STRAIGHT	-	20.000
END	153.304	318453.173	6247199.788	145°00'00"	-	-	-

CONTROL LINE MC00 - VERTICAL ALIGNMENT

PVI	CHAINAGE	RL	GRADE IN %	GRADE OUT %	CURVE L	K VALUE	TYPE
PVI00	0.000	15.694	-	+0.442	-	-	-
PVI01	110.000	16.180	+0.442	-3.543	70.000	17.57	CREST
PVI02	220.000	12.283	-3.543	-1.866	80.000	47.72	SAG
PVI03	330.000	10.230	-1.866	+2.205	90.000	22.11	SAG
PVI04	440.000	12.655	+2.205	-1.361	90.000	25.24	CREST
PVI05	540.000	11.294	-1.361	-1.100	90.000	344.83	SAG
PVI06	640.000	10.194	-1.100	+3.594	90.000	19.17	SAG
PVI07	740.000	13.788	+3.594	+2.098	90.000	60.16	CREST
PVI08	840.000	15.886	+2.098	-1.025	90.000	28.82	CREST
PVI09	940.000	14.861	-1.025	-4.314	80.000	24.32	CREST
PVI10	1040.000	10.547	-4.314	-	-	-	-

CONTROL LINE MC01 - VERTICAL ALIGNMENT

PVI	CHAINAGE	RL	GRADE IN %	GRADE OUT %	CURVE L	K VALUE	TYPE
PVI00	0.000	15.711	-	-2.444	-	-	-
PVI01	45.000	14.611	-2.444	-2.862	40.000	95.72	CREST
PVI02	153.304	11.511	-2.862	-	-	-	-

MC00 STATIONS AT 20 m (1 OF 2)

CHAINAGE	EASTING	NORTHING	BEARING	DESIGN RL
0.000	318310.000	6247345.000	90°00'00"	15.694
20.000	318330.000	6247345.000	90°00'00"	15.782
40.000	318350.000	6247345.000	90°00'00"	15.871
60.000	318370.000	6247345.000	90°00'00"	15.959
80.000	318390.000	6247345.000	90°00'00"	16.040
100.000	318410.000	6247345.000	90°00'00"	15.958
120.000	318430.000	6247345.000	90°00'00"	15.648
140.000	318450.000	6247345.000	90°00'00"	15.110
160.000	318470.000	6247345.000	90°00'00"	14.409
180.000	318490.000	6247345.000	90°00'00"	13.700
200.000	318510.000	6247345.000	90°00'00"	13.033
220.000	318530.000	6247345.000	90°00'00"	12.451
240.000	318550.000	6247345.000	90°00'00"	11.952
260.000	318570.000	6247345.000	90°00'00"	11.536
280.000	318590.000	6247345.000	90°00'00"	11.163
300.000	318610.000	6247345.000	90°00'00"	10.841
320.000	318630.000	6247345.000	90°00'00"	10.694
340.000	318649.991	6247344.643	94°05'33"	10.728
360.000	318669.771	6247341.798	102°16'40"	10.942
380.000	318688.944	6247336.166	110°27'46"	11.332
400.000	318707.120	6247327.862	118°38'52"	11.768
420.000	318723.928	6247317.054	126°49'59"	12.090
440.000	318739.026	6247303.964	135°01'05"	12.254
460.000	318752.107	6247288.857	143°12'12"	12.259
480.000	318762.904	6247272.042	151°23'18"	12.106
500.000	318771.197	6247253.861	159°34'24"	11.839
520.000	318776.817	6247234.684	167°45'31"	11.575

MC00 STATIONS AT 20 m (2 OF 2)

CHAINAGE	EASTING	NORTHING	BEARING	DESIGN RL
540.000	318779.649	6247214.903	175°56'37"	11.323
560.000	318780.000	6247194.911	180°00'00"	11.083
580.000	318780.000	6247174.911	180°00'00"	10.854
600.000	318780.812	6247154.941	173°49'30"	10.641
620.000	318784.374	6247135.278	165°38'23"	10.577
640.000	318790.699	6247116.322	157°27'17"	10.722
660.000	318799.659	6247098.460	149°16'11"	11.076
680.000	318811.070	6247082.056	141°05'04"	11.638
700.000	318824.700	6247067.443	132°53'58"	12.348
720.000	318840.272	6247054.920	124°42'51"	13.017
740.000	318857.469	6247044.741	116°31'45"	13.620
760.000	318875.939	6247037.114	108°20'39"	14.156
780.000	318895.307	6247032.195	100°09'32"	14.625
800.000	318915.178	6247030.083	91°58'26"	15.042
820.000	318935.177	6247030.000	90°00'00"	15.358
840.000	318955.177	6247030.000	90°00'00"	15.535
860.000	318975.177	6247030.000	90°00'00"	15.573
880.000	318995.177	6247030.000	90°00'00"	15.472
900.000	319015.177	6247030.000	90°00'00"	15.271
920.000	319035.177	6247030.000	90°00'00"	14.984
940.000	319055.177	6247030.000	90°00'00"	14.532
960.000	319075.177	6247030.000	90°00'00"	13.916
980.000	319095.177	6247030.000	90°00'00"	13.135
1000.000	319115.177	6247030.000	90°00'00"	12.273
1020.000	319135.177	6247030.000	90°00'00"	11.410
1040.000	319155.177	6247030.000	90°00'00"	10.547

CLIENT

NORTHGATE
REGIONAL COUNCIL
Infrastructure Delivery | Roads & Drainage

PROJECT

PROJECT No 25-0412

KESTREL ROAD UPGRADE

STAGE 2

Marlow Street to Ironbark Avenue
Northgate NSW 2217

DESIGN PACKAGE RW01 | ROADWORKS

PREPARED BY

MERIDIAN
CIVIL CONSULTING
Level 9, 140 Harbour Street, Sydney NSW 2000
Tel: +61 2 5550 0142
meridiancivil.example

DRAWING TITLE

SETOUT TABLES

CONTROL LINES MC00 AND MC01

SHEET 1 OF 1

DRAWING No.

KRU2-MCC-0412-RW-DRG-000056

REV	STATUS / SUITABILITY	ISSUE DATE
C	S3 FOR REVIEW AND COMMENT Not for construction	30.10.26

EDMS No	SHEET SIZE	SCALE @ A1
DS2026/01877	A1	NTS

REV	DESCRIPTION	BY	CHK	APP	DATE
A	50% DETAILED DESIGN	AN	SI	TM	28.05.26
B	80% DETAILED DESIGN	AN	SI	TM	14.08.26
C	100% DETAILED DESIGN	AN	SI	TM	30.10.26

ROLE	NAME	INITIALS	DATE
DRAWN	AMINA NGUYEN	AN	30.10.26
DESIGNED	RAFAEL OKAFOR	RO	30.10.26
DRAWING CHECK	LENA HARTMANN	LH	30.10.26
DESIGN CHECK	SANJAY IYER	SI	30.10.26
PROJECT MANAGER	DEIRDRE KOWALSKI	DK	30.10.26
APPROVED	TOBY McALLISTER	TM	30.10.26

COORDINATE SYSTEM	HEIGHT DATUM
GDA2020 / MGA ZONE 56	AHD71
DISCIPLINE	DESIGN LOT CODE
ROADWORKS	LOT-03
CONTRACT No	BRIDGE / ASSET No
NRC-C-2026-014	N/A
REFERENCES	AMENDMENT No
KRU2-MCC-0412-GN-M2D-000001	AMD-0006

SCAN FOR LATEST REV

COPYRIGHT AND DISCLAIMER
This drawing and the related information have been prepared by, or at the request of, Northgate Regional Council for a specific purpose and may not be used for any purpose other than the purpose intended. Northgate Regional Council does not provide any warranties and accepts no liability arising out of the use of this drawing for any other purpose. This drawing is protected by copyright and no part may be reproduced in any form without the express written permission of Northgate Regional Council.

DRAWING COLOUR CODED - PRINT ALL COPIES IN COLOUR


FILE NAME	PLOT DATE & TIME
KRU2-MCC-0412-RW-DRG-000056.dwg	30/10/2026 4:12:05 PM

LEGEND

- DESIGN SURFACE
- EXISTING SURFACE
- PROPOSED DRAINAGE
- EXISTING SEWER / WATER MAIN
- EXISTING UNDERGROUND POWER
- EXISTING TELECOMMUNICATIONS
- STRUCTURE (SHOWN INDICATIVELY)

NOTES

1. FOR ROADWORKS ALIGNMENT CONTROL PLANS REFER TO DRAWINGS RW-DRG-000031 TO 000034.
2. FOR CROSS SECTIONS REFER TO DRAWINGS RW-DRG-000301 TO 000305.
3. VERTICAL EXAGGERATION 5:1. LEVELS ARE IN METRES AHD71.

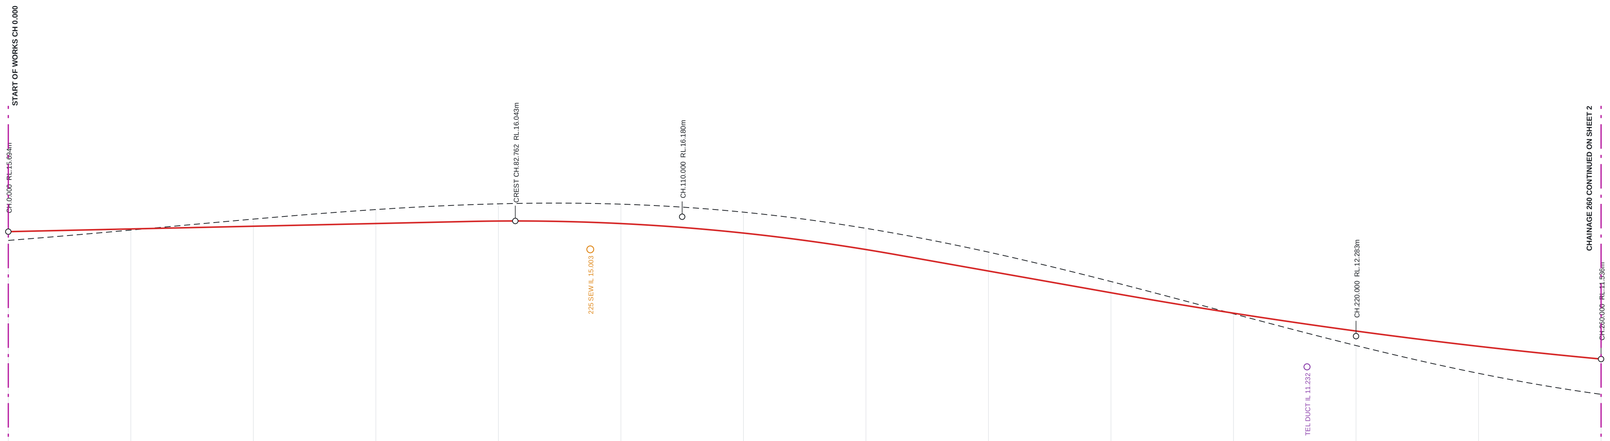

VERTICAL ALIGNMENT	G=+0.442%																G=-3.543%									
																K=17.568 L=70.000								K=47.722 L=80.000		
HORIZONTAL ALIGNMENT	L=330.000																									
CROSSFALL	LHS -3.0% RHS -3.0%																									
DESIGN LEVELS	15.604	15.738	15.782	15.827	15.871	15.915	15.959	16.003	16.040	16.028	15.958	15.831	15.648	15.407	15.110	14.763	14.409	14.054	13.700	13.356	13.033	12.732	12.451	12.191	11.962	11.734	11.516
EXISTING LEVELS	15.408	15.571	15.745	15.926	16.104	16.270	16.415	16.529	16.602	16.625	16.591	16.494	16.331	16.099	15.802	15.442	15.027	14.564	14.066	13.544	13.013	12.485	11.977	11.501	11.070	10.695	10.385
CHAINAGE	0.000	10.000	20.000	30.000	40.000	50.000	60.000	70.000	80.000	90.000	100.000	110.000	120.000	130.000	140.000	150.000	160.000	170.000	180.000	190.000	200.000	210.000	220.000	230.000	240.000	250.000	260.000


DESIGN CONTROL - MC00 - KESTREL ROAD

CHAINAGE 0.000 TO 260.000

0 10 20 40m
HORIZONTAL SCALE 1:500 @A1

0 1 2 4m
VERTICAL SCALE 1:100 @A1

KEY PLAN NOT TO SCALE

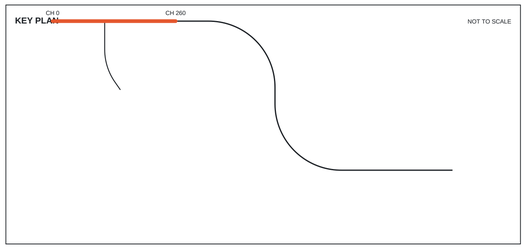

CLIENT

NORTHGATE REGIONAL COUNCIL
Infrastructure Delivery | Roads & Drainage

PROJECT PROJECT No 25-0412

KESTREL ROAD UPGRADE

STAGE 2

Marlow Street to Ironbark Avenue
Northgate NSW 2217

DESIGN PACKAGE RW01 | ROADWORKS

PREPARED BY

MERIDIAN
CIVIL CONSULTING
Level 9, 140 Harbour Street, Sydney NSW 2000
Tel: +61 2 5550 0142
meridiancivil.example

DRAWING TITLE

LONGITUDINAL SECTION

CONTROL LINE MC00 CH 0-260

SHEET 1 OF 4

DRAWING No.

KRU2-MCC-0412-RW-DRG-000201

REV	STATUS / SUITABILITY	ISSUE DATE
C	S3 FOR REVIEW AND COMMENT Not for construction	30.10.26

EDMS No	SHEET SIZE	SCALE @ A1
DS2026/01877	A1	AS SHOWN

REV	DESCRIPTION	BY	CHK	APP	DATE
A	50% DETAILED DESIGN	AN	SI	TM	28.05.26
B	80% DETAILED DESIGN	AN	SI	TM	14.08.26
C	100% DETAILED DESIGN	AN	SI	TM	30.10.26

ROLE	NAME	INITIALS	DATE
DRAWN	AMINA NGUYEN	AN	30.10.26
DESIGNED	RAFAEL OKAFOR	RO	30.10.26
DRAWING CHECK	LENA HARTMANN	LH	30.10.26
DESIGN CHECK	SANJAY IYER	SI	30.10.26
PROJECT MANAGER	DEIRDRE KOWALSKI	DK	30.10.26
APPROVED	TOBY McALLISTER	TM	30.10.26

COORDINATE SYSTEM	HEIGHT DATUM
GDA2020 / MGA ZONE 56	AHD71
DISCIPLINE	DESIGN LOT CODE
ROADWORKS	LOT-03
CONTRACT No	BRIDGE / ASSET No
NRC-C-2026-014	N/A
REFERENCES	AMENDMENT No
KRU2-MCC-0412-GN-M2D-000001	AMD-0006

COPYRIGHT AND DISCLAIMER

This drawing and the related information have been prepared by, or at the request of, Northgate Regional Council for a specific purpose and may not be used for any purpose other than the purpose intended. Northgate Regional Council does not provide any warranties and accepts no liability arising out of the use of this drawing for any other purpose. This drawing is protected by copyright and no part may be reproduced in any form without the express written permission of Northgate Regional Council.

SCAN FOR LATEST REV

DRAWING COLOUR CODED - PRINT ALL COPIES IN COLOUR


FILE NAME	PLOT DATE & TIME
KRU2-MCC-0412-RW-DRG-000201.dwg	30/10/2026 4:12:05 PM

LEGEND

- DESIGN SURFACE
- EXISTING SURFACE
- PROPOSED DRAINAGE
- EXISTING SEWER / WATER MAIN
- EXISTING UNDERGROUND POWER
- EXISTING TELECOMMUNICATIONS
- STRUCTURE (SHOWN INDICATIVELY)

NOTES

1. FOR ROADWORKS ALIGNMENT CONTROL PLANS REFER TO DRAWINGS RW-DRG-000031 TO 000034.
2. FOR CROSS SECTIONS REFER TO DRAWINGS RW-DRG-000301 TO 000305.
3. VERTICAL EXAGGERATION 5:1. LEVELS ARE IN METRES AHD71.

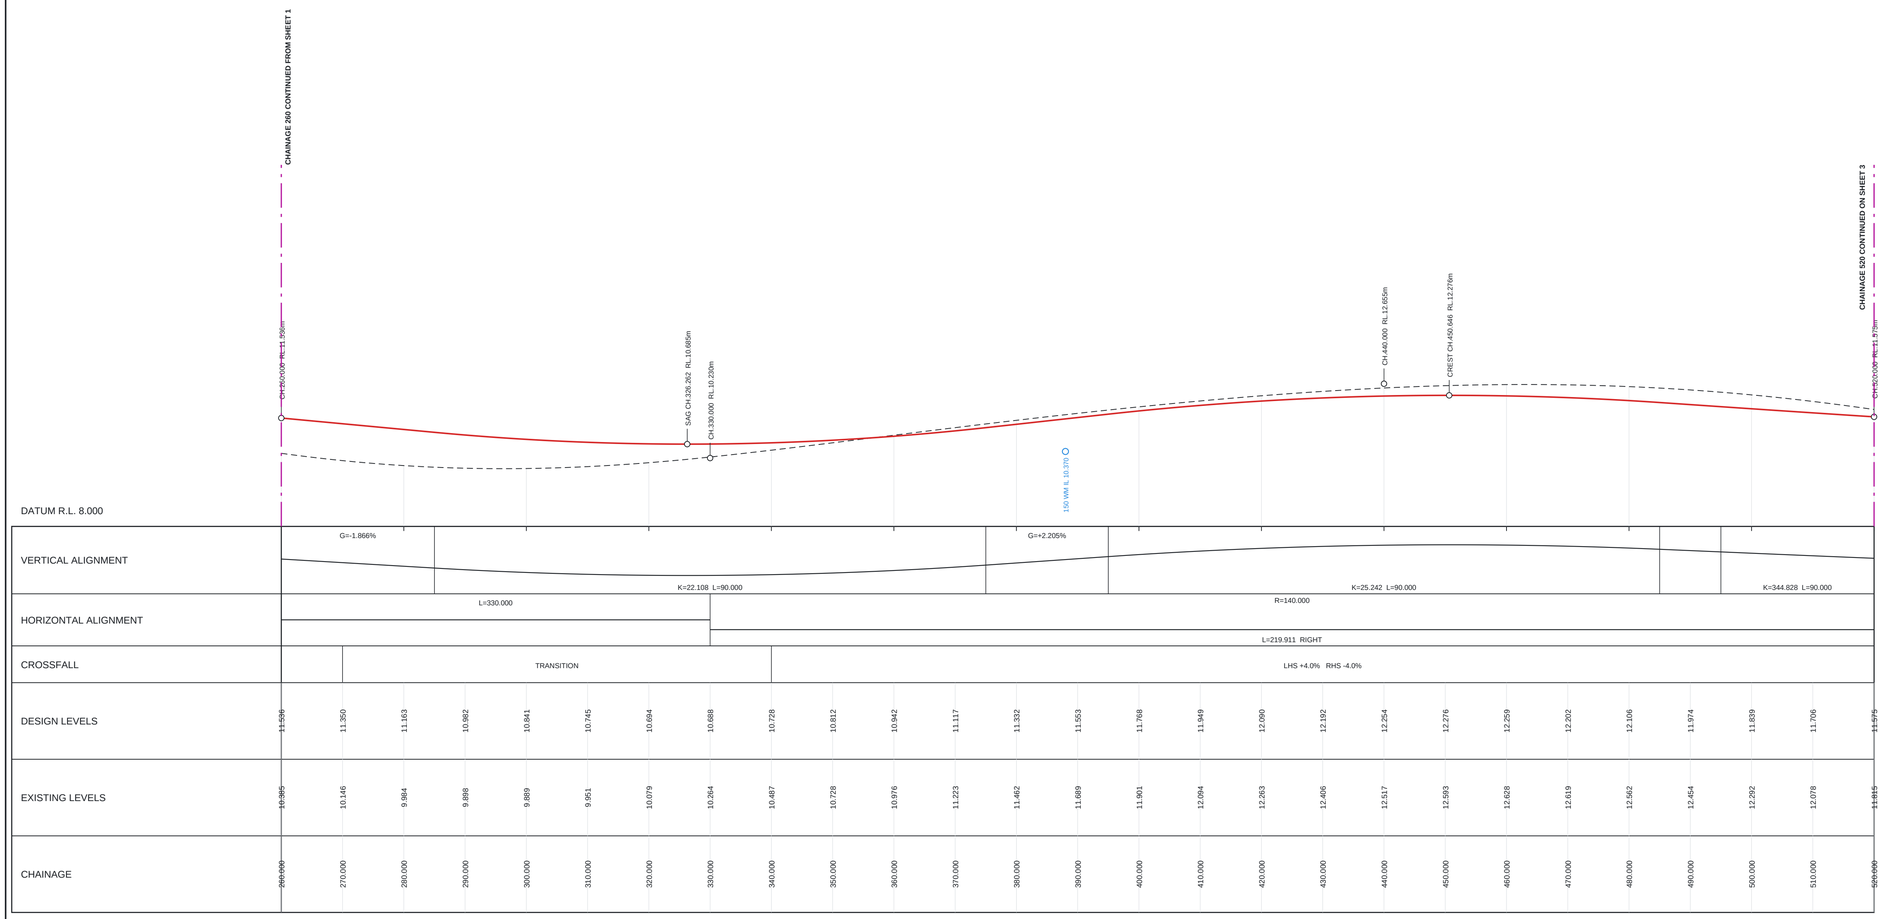


DESIGN CONTROL - MC00 - KESTREL ROAD

CHAINAGE 260.000 TO 520.000

0 10 20 40m
HORIZONTAL SCALE 1:500 @A1

0 1 2 4m
VERTICAL SCALE 1:100 @A1

KEY PLAN NOT TO SCALE

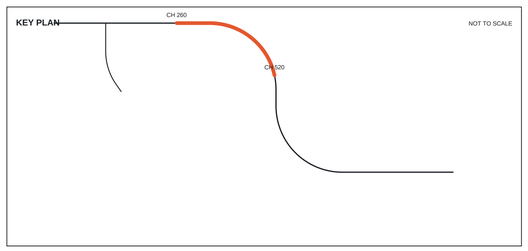

CLIENT

NORTHGATE REGIONAL COUNCIL
Infrastructure Delivery | Roads & Drainage

PROJECT PROJECT No 25-0412

KESTREL ROAD UPGRADE

STAGE 2

Marlow Street to Ironbark Avenue
Northgate NSW 2217

DESIGN PACKAGE RW01 | ROADWORKS

PREPARED BY

MERIDIAN
CIVIL CONSULTING
Level 9, 140 Harbour Street, Sydney NSW 2000
Tel: +61 2 5550 0142
meridiancivil.example

DRAWING TITLE

LONGITUDINAL SECTION

CONTROL LINE MC00 CH 260-520

SHEET 2 OF 4

DRAWING No.

KRU2-MCC-0412-RW-DRG-000202

REV	STATUS / SUITABILITY	ISSUE DATE
C	S3 FOR REVIEW AND COMMENT Not for construction	30.10.26

EDMS No	SHEET SIZE	SCALE @ A1
DS2026/01877	A1	AS SHOWN

REV	DESCRIPTION	BY	CHK	APP	DATE
A	50% DETAILED DESIGN	AN	SI	TM	28.05.26
B	80% DETAILED DESIGN	AN	SI	TM	14.08.26
C	100% DETAILED DESIGN	AN	SI	TM	30.10.26

ROLE	NAME	INITIALS	DATE
DRAWN	AMINA NGUYEN	AN	30.10.26
DESIGNED	RAFAEL OKAFOR	RO	30.10.26
DRAWING CHECK	LENA HARTMANN	LH	30.10.26
DESIGN CHECK	SANJAY IYER	SI	30.10.26
PROJECT MANAGER	DEIRDRE KOWALSKI	DK	30.10.26
APPROVED	TOBY McALLISTER	TM	30.10.26


COORDINATE SYSTEM	HEIGHT DATUM
GDA2020 / MGA ZONE 56	AHD71
DISCIPLINE	DESIGN LOT CODE
ROADWORKS	LOT-03
CONTRACT No	BRIDGE / ASSET No
NRC-C-2026-014	N/A
REFERENCES	AMENDMENT No
KRU2-MCC-0412-GN-M2D-000001	AMD-0006

COPYRIGHT AND DISCLAIMER
This drawing and the related information have been prepared by, or at the request of, Northgate Regional Council for a specific purpose and may not be used for any purpose other than the purpose intended. Northgate Regional Council does not provide any warranties and accepts no liability arising out of the use of this drawing for any other purpose. This drawing is protected by copyright and no part may be reproduced in any form without the express written permission of Northgate Regional Council.

SCAN FOR LATEST REV

DRAWING COLOUR CODED - PRINT ALL COPIES IN COLOUR

FILE NAME	PLOT DATE & TIME
KRU2-MCC-0412-RW-DRG-000202.dwg	30/10/2026 4:12:05 PM

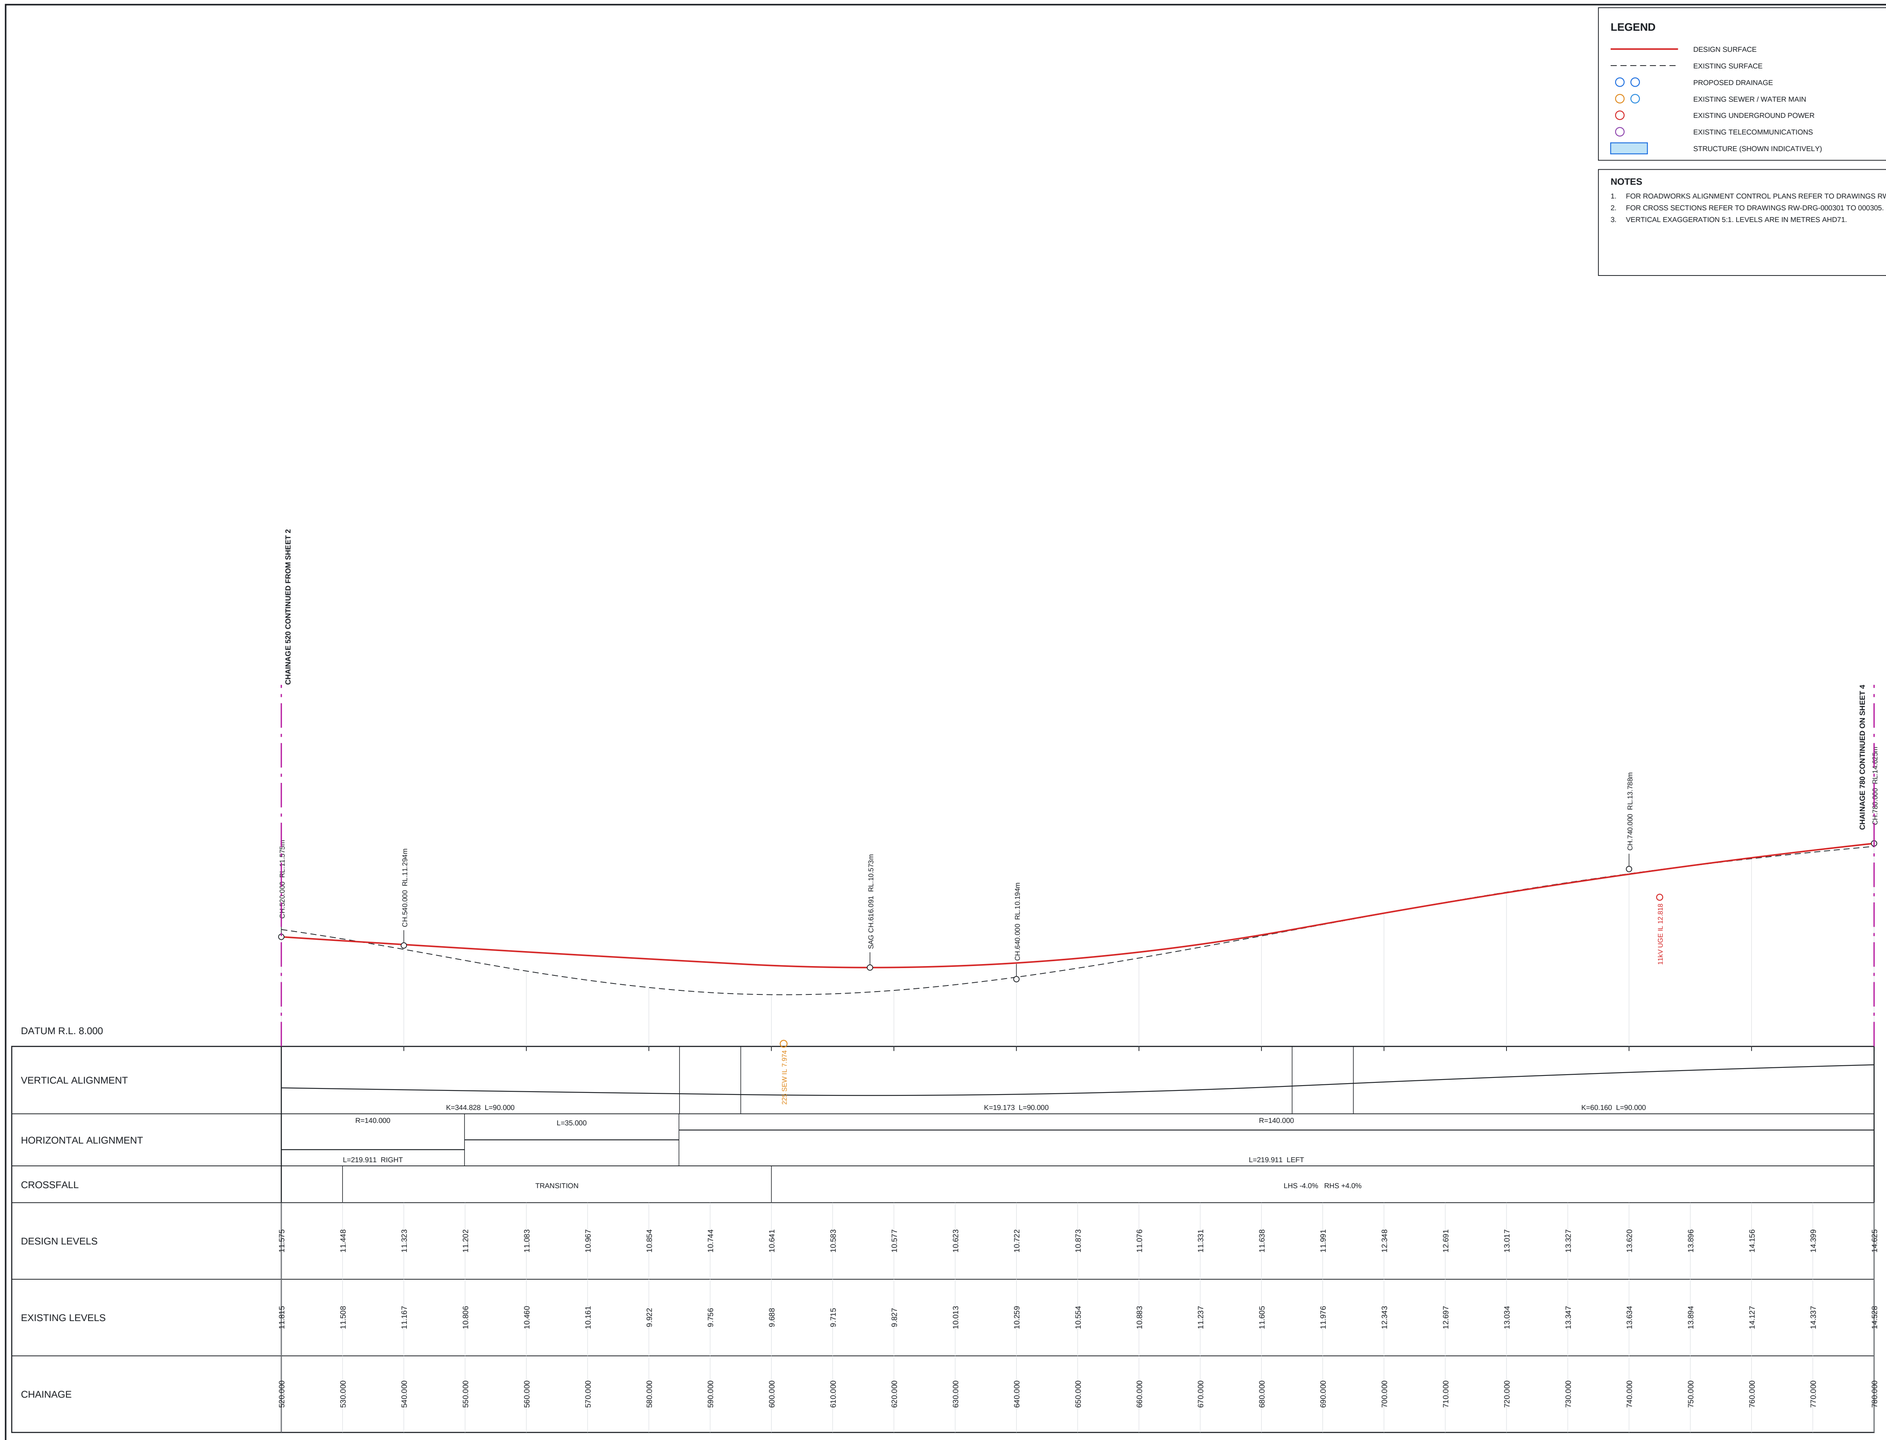


DESIGN CONTROL - MC00 - KESTREL ROAD

CHAINAGE 520.000 TO 780.000

HORIZONTAL SCALE 1:500 @A1 (0, 10, 20, 40m)

VERTICAL SCALE 1:100 @A1 (0, 1, 2, 4m)

KEY PLAN NOT TO SCALE

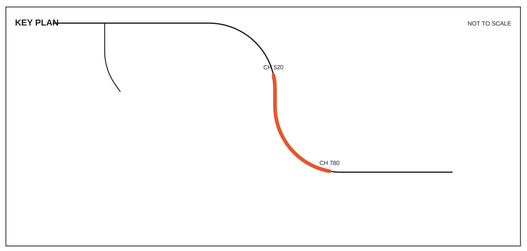

LEGEND

- DESIGN SURFACE
- EXISTING SURFACE
- PROPOSED DRAINAGE
- EXISTING SEWER / WATER MAIN
- EXISTING UNDERGROUND POWER
- EXISTING TELECOMMUNICATIONS
- STRUCTURE (SHOWN INDICATIVELY)

NOTES

1. FOR ROADWORKS ALIGNMENT CONTROL PLANS REFER TO DRAWINGS RW-DRG-000031 TO 000034.
2. FOR CROSS SECTIONS REFER TO DRAWINGS RW-DRG-000301 TO 000305.
3. VERTICAL EXAGGERATION 5:1. LEVELS ARE IN METRES AHD71.

CLIENT

NORTHGATE REGIONAL COUNCIL
Infrastructure Delivery | Roads & Drainage

PROJECT — PROJECT No 25-0412

KESTREL ROAD UPGRADE

STAGE 2

Marlow Street to Ironbark Avenue
Northgate NSW 2217

DESIGN PACKAGE RW01 | ROADWORKS

PREPARED BY

MERIDIAN
CIVIL CONSULTING

Level 9, 140 Harbour Street, Sydney NSW 2000
Tel: +61 2 5550 0142
meridiancivil.example

DRAWING TITLE

LONGITUDINAL SECTION

CONTROL LINE MC00 CH 520-780

SHEET 3 OF 4

DRAWING No.

KRU2-MCC-0412-RW-DRG-000203

REV	STATUS / SUITABILITY	ISSUE DATE
C	S3 FOR REVIEW AND COMMENT — Not for construction	30.10.26

EDMS No	SHEET SIZE	SCALE @ A1
DS2026/01877	A1	AS SHOWN

REV	DESCRIPTION	BY	CHK	APP	DATE
A	50% DETAILED DESIGN	AN	SI	TM	28.05.26
B	80% DETAILED DESIGN	AN	SI	TM	14.08.26
C	100% DETAILED DESIGN	AN	SI	TM	30.10.26

ROLE	NAME	INITIALS	DATE
DRAWN	AMINA NGUYEN	AN	30.10.26
DESIGNED	RAFAEL OKAFOR	RO	30.10.26
DRAWING CHECK	LENA HARTMANN	LH	30.10.26
DESIGN CHECK	SANJAY IYER	SI	30.10.26
PROJECT MANAGER	DEIRDRE KOWALSKI	DK	30.10.26
APPROVED	TOBY McALLISTER	TM	30.10.26

COORDINATE SYSTEM	HEIGHT DATUM
GDA2020 / MGA ZONE 56	AHD71
DISCIPLINE	DESIGN LOT CODE
ROADWORKS	LOT-03
CONTRACT No	BRIDGE / ASSET No
NRC-C-2026-014	N/A
REFERENCES	AMENDMENT No
KRU2-MCC-0412-GN-M2D-000001	AMD-0006

COPYRIGHT AND DISCLAIMER

This drawing and the related information have been prepared by, or at the request of, Northgate Regional Council for a specific purpose and may not be used for any purpose other than the purpose intended. Northgate Regional Council does not provide any warranties and accepts no liability arising out of the use of this drawing for any other purpose. This drawing is protected by copyright and no part may be reproduced in any form without the express written permission of Northgate Regional Council.

SCAN FOR LATEST REV

DRAWING COLOUR CODED - PRINT ALL COPIES IN COLOUR


FILE NAME	PLOT DATE & TIME
KRU2-MCC-0412-RW-DRG-000203.dwg	30/10/2026 4:12:05 PM

LEGEND

- DESIGN SURFACE
- EXISTING SURFACE
- PROPOSED DRAINAGE
- EXISTING SEWER / WATER MAIN
- EXISTING UNDERGROUND POWER
- EXISTING TELECOMMUNICATIONS
- STRUCTURE (SHOWN INDICATIVELY)


NOTES

1. FOR ROADWORKS ALIGNMENT CONTROL PLANS REFER TO DRAWINGS RW-DRG-000031 TO 000034.
2. FOR CROSS SECTIONS REFER TO DRAWINGS RW-DRG-000301 TO 000305.
3. VERTICAL EXAGGERATION 5:1. LEVELS ARE IN METRES AHD71.

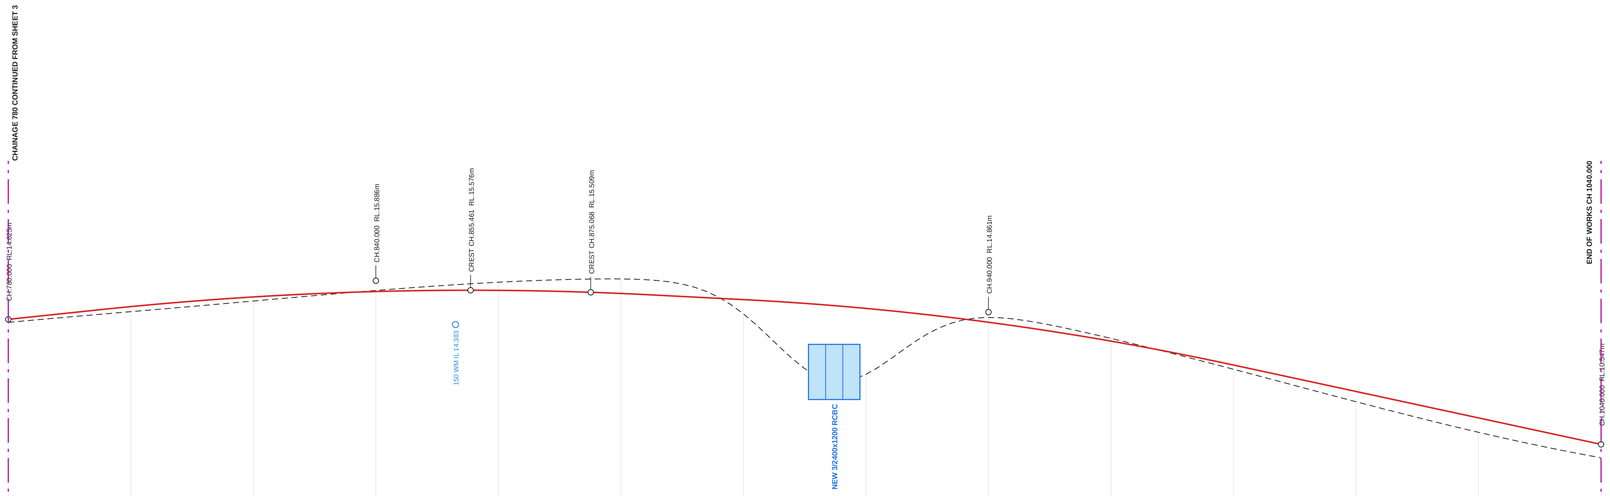

DATUM R.L. 8.000

| | | |

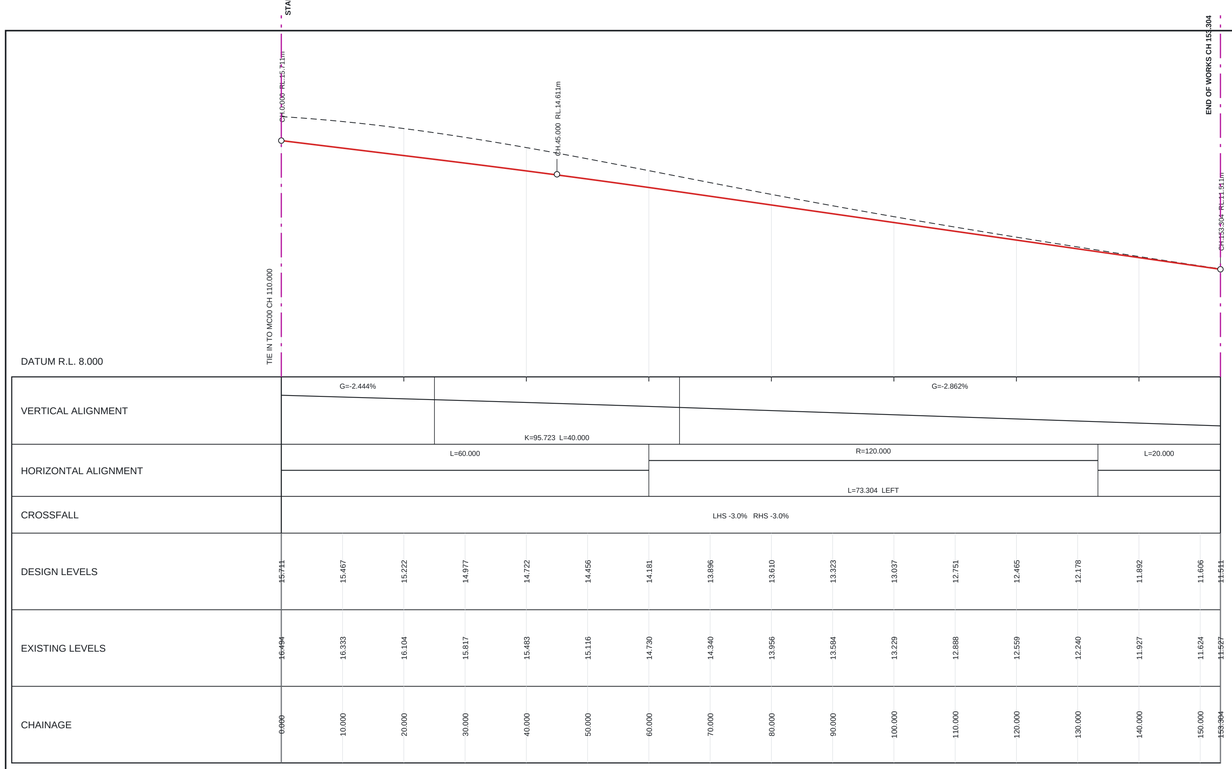


DATUM R.L. 8.000

VERTICAL ALIGNMENT	G=-2.444%										G=-2.862%											
											K=95.723 L=40.000											
HORIZONTAL ALIGNMENT	L=60.000								R=120.000										L=20.000			
											L=73.304 LEFT											
CROSSFALL	LHS -3.0% RHS -3.0%																					
DESIGN LEVELS	15.711	15.467	15.222	14.977	14.722	14.456	14.181	13.896	13.610	13.323	13.037	12.751	12.465	12.178	11.892	11.606	11.541					
EXISTING LEVELS	16.494	16.333	16.104	15.817	15.483	15.116	14.730	14.340	13.956	13.584	13.229	12.888	12.559	12.240	11.927	11.624	11.527					
CHAINAGE	0.000	10.000	20.000	30.000	40.000	50.000	60.000	70.000	80.000	90.000	100.000	110.000	120.000	130.000	140.000	150.000	153.304					

DESIGN CONTROL - MC01 - HARTLEY STREET

CHAINAGE 0.000 TO 153.304

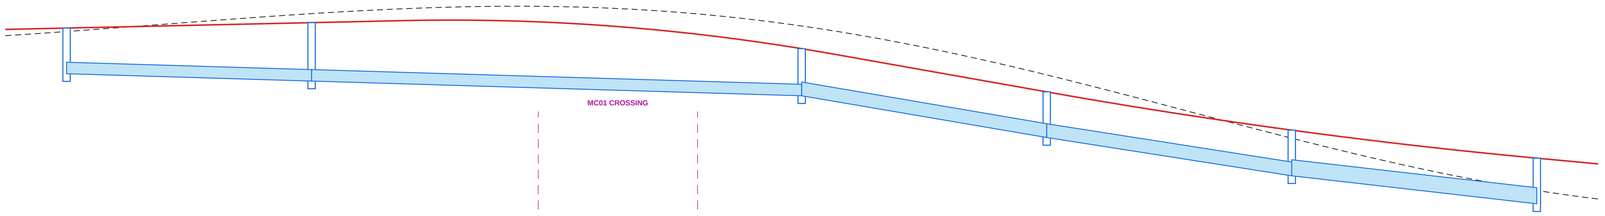

DATUM R.L. 9.000

PIT No	D01-01				D01-02							D01-03							D01-04			
PIPE SIZE / GRADE	375 dia RCP 0.60% / L=40.0							375 dia RCP 0.60% / L=80.0							450 dia RCP 3.41% / L=40.0							
PIPE INVERT LEVEL	14.232				13.992							13.512							12.150			
KERB / EXISTING LEVEL	15.722 / 15.610	15.767 / 15.757	15.811 / 15.909	15.855 / 16.058	15.899 / 16.194	15.943 / 16.308	15.987 / 16.390	15.868 / 16.432	15.898 / 16.424	15.771 / 16.360	15.880 / 16.235	15.347 / 16.045	15.050 / 15.790	14.703 / 15.471	14.349 / 15.094	13.994 / 14.665	13.640 / 14.194	13.296 / 13.691	12.973 / 13.170	12.672 / 12.644	12.391 / 12.127	12.131 / 11.634
CHAINAGE	20.000	30.000	40.000	50.000	60.000	70.000	80.000	90.000	100.000	110.000	120.000	130.000	140.000	150.000	160.000	170.000	180.000	190.000	200.000	210.000	220.000	230.000

PIT No	D01-05						D01-06															
PIPE SIZE / GRADE	525 dia RCP 2.29% / L=40.0																					
PIPE INVERT LEVEL	10.901						9.986															
KERB / EXISTING LEVEL	11.892 / 11.177	11.674 / 10.770	11.476 / 10.423	11.292 / 10.144																		
CHAINAGE	240.000	250.000	260.000	270.000																		

DRAINAGE LONGITUDINAL SECTION - LINE D01

RIGHT KERB MC00 CH 20 TO CH 260

LEGEND

- DESIGN SURFACE
- EXISTING SURFACE
- PROPOSED DRAINAGE
- EXISTING SEWER / WATER MAIN
- EXISTING UNDERGROUND POWER
- EXISTING TELECOMMUNICATIONS
- STRUCTURE (SHOWN INDICATIVELY)

NOTES

1. FOR ROADWORKS GENERAL ARRANGEMENT PLANS REFER TO DRAWINGS RW-DRG-000031 TO 000034.
2. FOR MC00 LONGITUDINAL SECTIONS REFER TO DRAWINGS RW-DRG-000201 TO 000204.
3. PIPE INVERT LEVELS ARE TO THE PIT WALL.

0 10 20 40m
HORIZONTAL SCALE 1:500 @A1

0 1 2 4m
VERTICAL SCALE 1:100 @A1

CLIENT

NORTHGATE REGIONAL COUNCIL
Infrastructure Delivery | Roads & Drainage

PROJECT

PROJECT No 25-0412

KESTREL ROAD UPGRADE

STAGE 2

Marlow Street to Ironbark Avenue
Northgate NSW 2217

DESIGN PACKAGE RW01 | ROADWORKS

PREPARED BY

MERIDIAN
CIVIL CONSULTING
Level 9, 140 Harbour Street, Sydney NSW 2000
Tel: +61 2 5550 0142
meridiancivil.example

DRAWING TITLE

LONGITUDINAL SECTIONS

MC01 AND DRAINAGE LINE D01

SHEET 1 OF 1

DRAWING No.

KRU2-MCC-0412-RW-DRG-000221

REV	STATUS / SUITABILITY	ISSUE DATE
C	S3 FOR REVIEW AND COMMENT Not for construction	30.10.26

EDMS No	SHEET SIZE	SCALE @ A1
DS2026/01877	A1	AS SHOWN

REV	DESCRIPTION	BY	CHK	APP	DATE
A	50% DETAILED DESIGN	AN	SI	TM	28.05.26
B	80% DETAILED DESIGN	AN	SI	TM	14.08.26
C	100% DETAILED DESIGN	AN	SI	TM	30.10.26

ROLE	NAME	INITIALS	DATE
DRAWN	AMINA NGUYEN	AN	30.10.26
DESIGNED	RAFAEL OKAFOR	RO	30.10.26
DRAWING CHECK	LENA HARTMANN	LH	30.10.26
DESIGN CHECK	SANJAY IYER	SI	30.10.26
PROJECT MANAGER	DEIRDRE KOWALSKI	DK	30.10.26
APPROVED	TOBY McALLISTER	TM	30.10.26


COORDINATE SYSTEM	HEIGHT DATUM
GDA2020 / MGA ZONE 56	AHD71
DISCIPLINE	DESIGN LOT CODE
ROADWORKS	LOT-03
CONTRACT No	BRIDGE / ASSET No
NRC-C-2026-014	N/A
REFERENCES	AMENDMENT No
KRU2-MCC-0412-GN-M2D-000001	AMD-0006

SCAN FOR LATEST REV

COPYRIGHT AND DISCLAIMER
This drawing and the related information have been prepared by, or at the request of, Northgate Regional Council for a specific purpose and may not be used for any purpose other than the purpose intended. Northgate Regional Council does not provide any warranties and accepts no liability arising out of the use of this drawing for any other purpose. This drawing is protected by copyright and no part may be reproduced in any form without the express written permission of Northgate Regional Council.

DRAWING COLOUR CODED - PRINT ALL COPIES IN COLOUR

FILE NAME	PLOT DATE & TIME
KRU2-MCC-0412-RW-DRG-000221.dwg	30/10/2026 4:12:05 PM

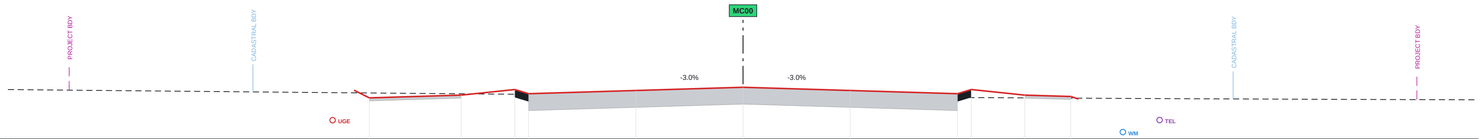


DATUM 14.0

	DAYLIGHT	PATH-OUT	PATH-IN	BOK	KERB	LANE	CL	LANE	KERB	BOK	PATH-IN	PATH-OUT	DAYLIGHT
DESIGN STRINGS													
DESIGN LEVELS	15.598	15.348	15.438	15.621	15.484	15.589	15.694	15.589	15.484	15.621	15.438	15.903	15.310
EXISTING LEVELS	15.513	15.508	15.482	15.467	15.463	15.434	15.408	15.383	15.361	15.358	15.348	15.340	15.338
DESIGN OFFSETS	-12.700	-12.200	-9.200	-7.450	-7.000	-3.500	0.000	3.500	7.000	7.450	9.200	10.700	10.950

CHAINAGE 0

SCALE 1:100

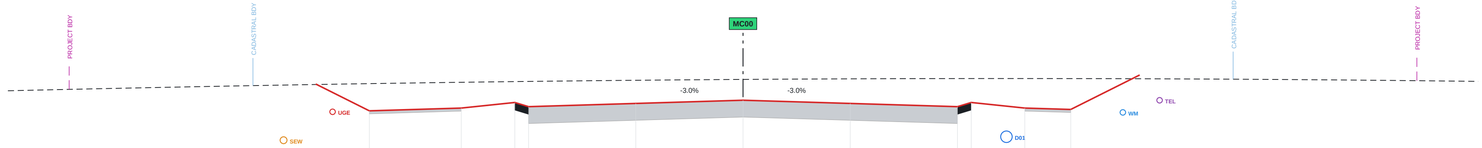


DATUM 14.0

	DAYLIGHT	PATH-OUT	PATH-IN	BOK	KERB	LANE	CL	LANE	KERB	BOK	PATH-IN	PATH-OUT	DAYLIGHT
DESIGN STRINGS													
DESIGN LEVELS	16.694	15.569	15.659	15.841	15.705	15.810	15.915	15.810	15.705	15.841	15.659	16.614	15.989
EXISTING LEVELS	16.589	16.543	16.480	16.442	16.432	16.352	16.270	16.185	16.098	16.087	16.043	16.005	15.985
DESIGN OFFSETS	-14.450	-12.200	-9.200	-7.450	-7.000	-3.500	0.000	3.500	7.000	7.450	9.200	10.700	11.450

CHAINAGE 50

SCALE 1:100

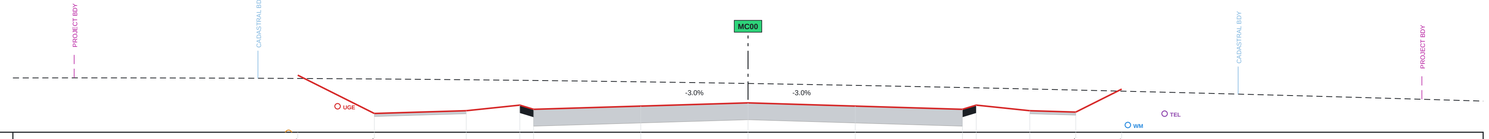

DATUM 15.0

	DAYLIGHT	PATH-OUT	PATH-IN	BOK	KERB	LANE	CL	LANE	KERB	BOK	PATH-IN	PATH-OUT	DAYLIGHT
DESIGN STRINGS													
DESIGN LEVELS	16.862	15.612	15.702	15.884	15.748	15.853	15.968	15.853	15.748	15.884	15.702	15.657	16.407
EXISTING LEVELS	16.755	16.739	16.713	16.694	16.689	16.645	16.591	16.529	16.469	16.449	16.411	16.376	16.340
DESIGN OFFSETS	-14.700	-12.200	-9.200	-7.450	-7.000	-3.500	0.000	3.500	7.000	7.450	9.200	10.700	12.200

CHAINAGE 100

SCALE 1:100

DATUM 13.0

	DAYLIGHT	PATH-OUT	PATH-IN	BOK	KERB	LANE	CL	LANE	KERB	BOK	PATH-IN	PATH-OUT	DAYLIGHT
DESIGN STRINGS													
DESIGN LEVELS	15.292	14.417	14.507	14.689	14.553	14.658	14.763	14.658	14.553	14.689	14.507	14.462	15.587
EXISTING LEVELS	15.276	15.304	15.348	15.371	15.377	15.414	15.442	15.461	15.470	15.471	15.471	15.469	15.464
DESIGN OFFSETS	-13.950	-12.200	-9.200	-7.450	-7.000	-3.500	0.000	3.500	7.000	7.450	9.200	10.700	12.950

CHAINAGE 150

SCALE 1:100

LEGEND

- EXISTING SURFACE
- DESIGN SURFACE
- NEW PAVEMENT
- KERB AND GUTTER
- PROPOSED DRAINAGE (D01)
- EXISTING SEWER (SEW)
- EXISTING WATER MAIN (WM)
- EXISTING UNDERGROUND POWER (UGE)
- EXISTING TELECOMMUNICATIONS (TEL)
- CADASTRAL BOUNDARY
- PROJECT BOUNDARY

NOTES

1. FOR ROADWORKS ALIGNMENT CONTROL PLANS REFER TO DRAWINGS RW-DRG-000031 TO 000034.
2. SECTIONS ARE VIEWED LOOKING UP CHAINAGE. LEFT IS ON THE LEFT.
3. LEVELS ARE IN METRES AHD71. OFFSETS ARE FROM CONTROL LINE MC00.

0 2 4 8m

SCALE 1:100 @A1

KEY PLAN

NOT TO SCALE

CLIENT

NORTHGATE REGIONAL COUNCIL
Infrastructure Delivery | Roads & Drainage

PROJECT

PROJECT No 25-0412

KESTREL ROAD UPGRADE

STAGE 2

Marlow Street to Ironbark Avenue
Northgate NSW 2217

DESIGN PACKAGE RW01 | ROADWORKS

PREPARED BY

MERIDIAN
CIVIL CONSULTING

Level 9, 140 Harbour Street, Sydney NSW 2000
Tel: +61 2 5550 0142
meridiancivil.example

DRAWING TITLE

CROSS SECTIONS

CONTROL LINE MC00 CH 0-150

SHEET 1 OF 5

DRAWING No.

KRU2-MCC-0412-RW-DRG-000301

REV	STATUS / SUITABILITY	ISSUE DATE
C	S3 FOR REVIEW AND COMMENT Not for construction	30.10.26

EDMS No	SHEET SIZE	SCALE @ A1
DS2026/01877	A1	1:100

REV	DESCRIPTION	BY	CHK	APP	DATE
A	50% DETAILED DESIGN	AN	SI	TM	28.05.26
B	80% DETAILED DESIGN	AN	SI	TM	14.08.26
C	100% DETAILED DESIGN	AN	SI	TM	30.10.26

ROLE	NAME	INITIALS	DATE
DRAWN	AMINA NGUYEN	AN	30.10.26
DESIGNED	RAFAEL OKAFOR	RO	30.10.26
DRAWING CHECK	LENA HARTMANN	LH	30.10.26
DESIGN CHECK	SANJAY IYER	SI	30.10.26
PROJECT MANAGER	DEIRDRE KOWALSKI	DK	30.10.26
APPROVED	TOBY McALLISTER	TM	30.10.26

COORDINATE SYSTEM	HEIGHT DATUM
GDA2020 / MGA ZONE 56	AHD71
DISCIPLINE	DESIGN LOT CODE
ROADWORKS	LOT-03
CONTRACT No	BRIDGE / ASSET No
NRC-C-2026-014	N/A
REFERENCES	AMENDMENT No
KRU2-MCC-0412-GN-M2D-000001	AMD-0006


SCAN FOR LATEST REV

COPYRIGHT AND DISCLAIMER

This drawing and the related information have been prepared by, or at the request of, Northgate Regional Council for a specific purpose and may not be used for any purpose other than the purpose intended. Northgate Regional Council does not provide any warranties and accepts no liability arising out of the use of this drawing for any other purpose. This drawing is protected by copyright and no part may be reproduced in any form without the express written permission of Northgate Regional Council.

DRAWING COLOUR CODED - PRINT ALL COPIES IN COLOUR

FILE NAME	PLOT DATE & TIME
KRU2-MCC-0412-RW-DRG-000301.dwg	30/10/2026 4:12:05 PM

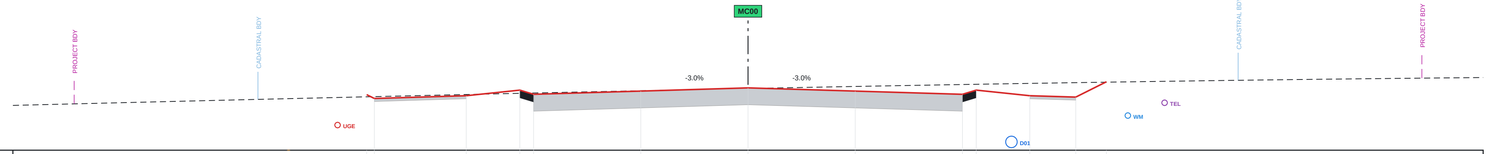


DATUM 11.0

DESIGN STRINGS	DAYLIGHT PATH-OUT	PATH-IN	BOK	KERB	LANE	CL	LANE	KERB	BOK	PATH-IN	PATH-OUT	DAYLIGHT		
DESIGN LEVELS	12.812 12.807	12.777	12.960	12.823	12.928	13.033	12.928	12.823	12.960	12.777	12.732	13.232		
EXISTING LEVELS	12.742 12.748	12.817	12.856	12.866	12.941	13.013	13.080	13.143	13.151	13.180	13.204	13.219		
DESIGN OFFSETS	-12.450 -12.200	-9.200	-7.450	-7.000	-3.500	0.000	3.500	7.000	7.450	9.200	10.700	11.700		

CHAINAGE 200

SCALE 1:100

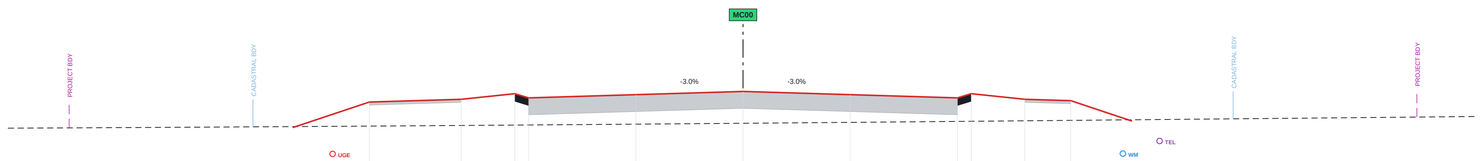


DATUM 9.0

DESIGN STRINGS	DAYLIGHT	PATH-OUT	PATH-IN	BOK	KERB	LANE	CL	LANE	KERB	BOK	PATH-IN	PATH-OUT	DAYLIGHT		
DESIGN LEVELS	10.554	11.388	11.478	11.660	11.524	11.629	11.734	11.629	11.524	11.660	11.478	11.433	10.766		
EXISTING LEVELS	10.586	10.602	10.623	10.636	10.639	10.666	10.695	10.724	10.756	10.760	10.776	10.789	10.808		
DESIGN OFFSETS	-14.700	-12.200	-9.200	-7.450	-7.000	-3.500	0.000	3.500	7.000	7.450	9.200	10.700	12.700		

CHAINAGE 250

SCALE 1:100

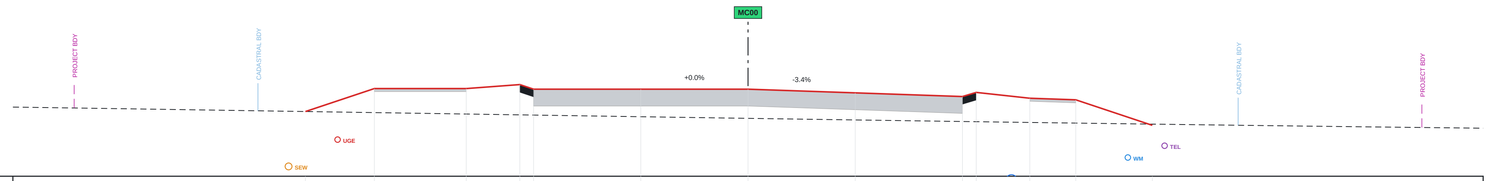

DATUM 8.0

DESIGN STRINGS	DAYLIGHT	PATH-OUT	PATH-IN	BOK	KERB	LANE	CL	LANE	KERB	BOK	PATH-IN	PATH-OUT	DAYLIGHT		
DESIGN LEVELS	10.111	10.861	10.861	10.991	10.841	10.841	10.841	10.721	10.601	10.735	10.545	10.494	9.661		
EXISTING LEVELS	10.111	10.077	10.030	10.003	9.996	9.942	9.889	9.837	9.786	9.780	9.755	9.734	9.700		
DESIGN OFFSETS	-14.450	-12.200	-9.200	-7.450	-7.000	-3.500	0.000	3.500	7.000	7.450	9.200	10.700	13.200		

CHAINAGE 300

SCALE 1:100



DATUM 9.0

DESIGN STRINGS	DAYLIGHT	PATH-OUT	PATH-IN	BOK	KERB	LANE	CL	LANE	KERB	BOK	PATH-IN	PATH-OUT DAYLIGHT		
DESIGN LEVELS	10.987	11.320	11.200	11.260	11.092	10.952	10.812	10.672	10.532	10.664	10.464	10.404 10.221		
EXISTING LEVELS	11.067	11.044	10.973	10.930	10.918	10.826	10.728	10.626	10.519	10.505	10.451	10.403 10.396		
DESIGN OFFSETS	-13.200	-12.200	-9.200	-7.450	-7.000	-3.500	0.000	3.500	7.000	7.450	9.200	10.700 10.950		

CHAINAGE 350

SCALE 1:100

LEGEND

- EXISTING SURFACE
- DESIGN SURFACE
- NEW PAVEMENT
- KERB AND GUTTER
- PROPOSED DRAINAGE (D01)
- EXISTING SEWER (SEW)
- EXISTING WATER MAIN (WM)
- EXISTING UNDERGROUND POWER (UGE)
- EXISTING TELECOMMUNICATIONS (TEL)
- CADASTRAL BOUNDARY
- PROJECT BOUNDARY

NOTES


1. FOR ROADWORKS ALIGNMENT CONTROL PLANS REFER TO DRAWINGS RW-DRG-000031 TO 000034.
2. SECTIONS ARE VIEWED LOOKING UP CHAINAGE. LEFT IS ON THE LEFT.
3. LEVELS ARE IN METRES AHD71. OFFSETS ARE FROM CONTROL LINE MC00.

0 2 4 8m

SCALE 1:100 @A1

KEY PLAN

NOT TO SCALE

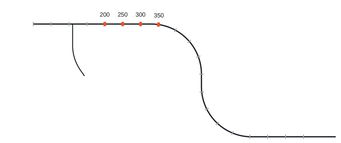

CLIENT

NORTHGATE REGIONAL COUNCIL
Infrastructure Delivery | Roads & Drainage

PROJECT

PROJECT No 25-0412

KESTREL ROAD UPGRADE

STAGE 2

Marlow Street to Ironbark Avenue
Northgate NSW 2217

DESIGN PACKAGE RW01 | ROADWORKS

PREPARED BY

MERIDIAN
CIVIL CONSULTING

Level 9, 140 Harbour Street, Sydney NSW 2000
Tel: +61 2 5550 0142
meridiancivil.example

DRAWING TITLE

CROSS SECTIONS

CONTROL LINE MC00 CH 200-350

SHEET 2 OF 5

DRAWING No.

KRU2-MCC-0412-RW-DRG-000302

REV	STATUS / SUITABILITY	ISSUE DATE
C	S3 FOR REVIEW AND COMMENT Not for construction	30.10.26

EDMS No	SHEET SIZE	SCALE @ A1
DS2026/01877	A1	1:100

REV	DESCRIPTION	BY	CHK	APP	DATE
A	50% DETAILED DESIGN	AN	SI	TM	28.05.26
B	80% DETAILED DESIGN	AN	SI	TM	14.08.26
C	100% DETAILED DESIGN	AN	SI	TM	30.10.26

ROLE	NAME	INITIALS	DATE
DRAWN	AMINA NGUYEN	AN	30.10.26
DESIGNED	RAFAEL OKAFOR	RO	30.10.26
DRAWING CHECK	LENA HARTMANN	LH	30.10.26
DESIGN CHECK	SANJAY IYER	SI	30.10.26
PROJECT MANAGER	DEIRDRE KOWALSKI	DK	30.10.26
APPROVED	TOBY McALLISTER	TM	30.10.26

COORDINATE SYSTEM	HEIGHT DATUM
GDA2020 / MGA ZONE 56	AHD71
DISCIPLINE	DESIGN LOT CODE
ROADWORKS	LOT-03
CONTRACT No	BRIDGE / ASSET No
NRC-C-2026-014	N/A
REFERENCES	AMENDMENT No
KRU2-MCC-0412-GN-M2D-000001	AMD-0006


SCAN FOR LATEST REV

COPYRIGHT AND DISCLAIMER

This drawing and the related information have been prepared by, or at the request of, Northgate Regional Council for a specific purpose and may not be used for any purpose other than the purpose intended. Northgate Regional Council does not provide any warranties and accepts no liability arising out of the use of this drawing for any other purpose. This drawing is protected by copyright and no part may be reproduced in any form without the express written permission of Northgate Regional Council.

DRAWING COLOUR CODED - PRINT ALL COPIES IN COLOUR

FILE NAME	PLOT DATE & TIME
KRU2-MCC-0412-RW-DRG-000302.dwg	30/10/2026 4:12:05 PM

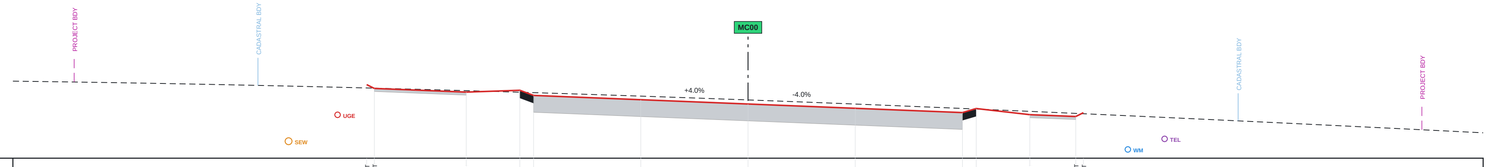


DATUM 10.0

	DAYLIGHT / PATH OUT	PATH IN	BOK	KERB	LANE	CL	LANE	KERB	BOK	PATH IN	PATH OUT / DAYLIGHT
DESIGN STRINGS											
DESIGN LEVELS	12.401 12.276	12.166	12.216	12.048	11.908	11.768	11.628	11.488	11.620	11.420	11.360 11.485
EXISTING LEVELS	12.392 12.266	12.204	12.153	12.139	12.025	11.901	11.767	11.623 11.604	11.604	11.528	11.462 11.451
DESIGN OFFSETS	-12.450 -12.200	-9.200	-7.450	-7.000	-3.500	0.000	3.500	7.000	7.450	9.200	10.700 10.950

CHAINAGE 400

SCALE 1:100

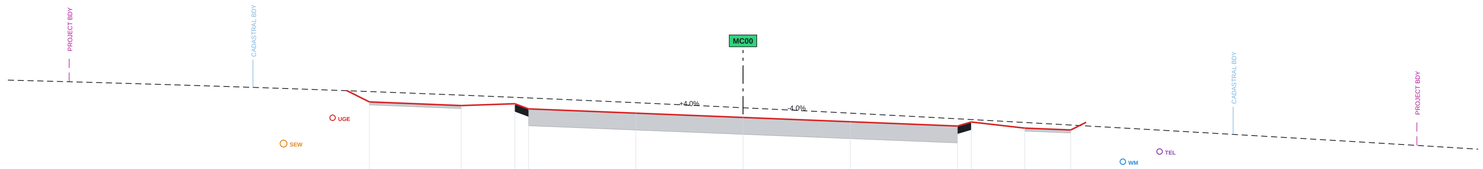


DATUM 10.0

	DAYLIGHT	PATH OUT	PATH IN	BOK	KERB	LANE	CL	LANE	KERB	BOK	PATH IN	PATH OUT	DAYLIGHT
DESIGN STRINGS													
DESIGN LEVELS	13.159	12.784	12.664	12.724	12.556	12.416	12.276	12.136	11.996	12.128	11.928	11.868	12.118
EXISTING LEVELS	13.150	13.122	13.005	12.932	12.913	12.758	12.593	12.417	12.233	12.208	12.112	12.029	12.000
DESIGN OFFSETS	-12.950	-12.200	-9.200	-7.450	-7.000	-3.500	0.000	3.500	7.000	7.450	9.200	10.700	11.200

CHAINAGE 450

SCALE 1:100

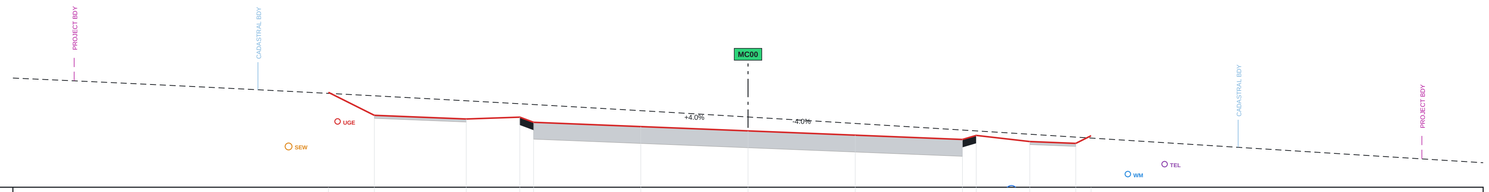


DATUM 10.0

	DAYLIGHT / PATH OUT	PATH IN	BOK	KERB	LANE	CL	LANE	KERB	BOK	PATH IN	PATH OUT / DAYLIGHT
DESIGN STRINGS											
DESIGN LEVELS	13.097	12.347	12.227	12.287	12.119	11.979	11.839	11.699	11.559	11.691	11.491	11.431	11.681
EXISTING LEVELS	13.063	12.984	12.821	12.724	12.699	12.488	12.292	12.081	11.866	11.838	11.729	11.635	11.604
DESIGN OFFSETS	-13.700	-12.200	-9.200	-7.450	-7.000	-3.500	0.000	3.500	7.000	7.450	9.200	10.700	11.200

CHAINAGE 500

SCALE 1:100

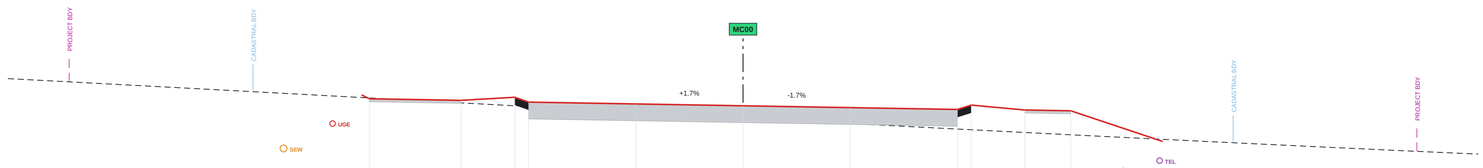

DATUM 9.0

	DAYLIGHT / PATH OUT	PATH IN	BOK	KERB	LANE	CL	LANE	KERB	BOK	PATH IN	PATH OUT	DAYLIGHT
DESIGN STRINGS												
DESIGN LEVELS	11.558 11.433	11.379	11.479	11.322	11.262	11.202	11.142	11.082	11.224	11.064	11.038	10.038
EXISTING LEVELS	11.471 11.457	11.296	11.202	11.178	10.991	10.806	10.623	10.442	10.419	10.331	10.255	10.107
DESIGN OFFSETS	-12.450 -12.200	-9.200	-7.450	-7.000	-3.500	0.000	3.500	7.000	7.450	9.200	10.700	13.700

CHAINAGE 550

SCALE 1:100

LEGEND

- EXISTING SURFACE
- DESIGN SURFACE
- NEW PAVEMENT
- KERB AND GUTTER
- PROPOSED DRAINAGE (D01)
- EXISTING SEWER (SEW)
- EXISTING WATER MAIN (WM)
- EXISTING UNDERGROUND POWER (UGE)
- EXISTING TELECOMMUNICATIONS (TEL)
- CADASTRAL BOUNDARY
- PROJECT BOUNDARY

NOTES


1. FOR ROADWORKS ALIGNMENT CONTROL PLANS REFER TO DRAWINGS RW-DRG-000031 TO 000034.
2. SECTIONS ARE VIEWED LOOKING UP CHAINAGE. LEFT IS ON THE LEFT.
3. LEVELS ARE IN METRES AHD71. OFFSETS ARE FROM CONTROL LINE MC00.

0 2 4 8m

SCALE 1:100 @A1

KEY PLAN

NOT TO SCALE

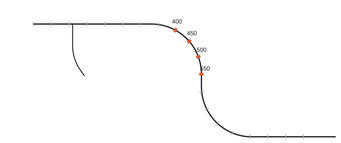

CLIENT

NORTHGATE REGIONAL COUNCIL
Infrastructure Delivery | Roads & Drainage

PROJECT

PROJECT No 25-0412

KESTREL ROAD UPGRADE

STAGE 2

Marlow Street to Ironbark Avenue
Northgate NSW 2217

DESIGN PACKAGE RW01 | ROADWORKS

PREPARED BY

MERIDIAN
CIVIL CONSULTING

Level 9, 140 Harbour Street, Sydney NSW 2000
Tel: +61 2 5550 0142
meridiancivil.example

DRAWING TITLE

CROSS SECTIONS

CONTROL LINE MC00 CH 400-550

SHEET 3 OF 5

DRAWING No.

KRU2-MCC-0412-RW-DRG-000303

REV	STATUS / SUITABILITY	ISSUE DATE
C	S3 FOR REVIEW AND COMMENT Not for construction	30.10.26

EDMS No	SHEET SIZE	SCALE @ A1
DS2026/01877	A1	1:100

REV	DESCRIPTION	BY	CHK	APP	DATE
A	50% DETAILED DESIGN	AN	SI	TM	28.05.26
B	80% DETAILED DESIGN	AN	SI	TM	14.08.26
C	100% DETAILED DESIGN	AN	SI	TM	30.10.26

ROLE	NAME	INITIALS	DATE
DRAWN	AMINA NGUYEN	AN	30.10.26
DESIGNED	RAFAEL OKAFOR	RO	30.10.26
DRAWING CHECK	LENA HARTMANN	LH	30.10.26
DESIGN CHECK	SANJAY IYER	SI	30.10.26
PROJECT MANAGER	DEIRDRE KOWALSKI	DK	30.10.26
APPROVED	TOBY McALLISTER	TM	30.10.26

COORDINATE SYSTEM	HEIGHT DATUM
GDA2020 / MGA ZONE 56	AHD71
DISCIPLINE	DESIGN LOT CODE
ROADWORKS	LOT-03
CONTRACT No	BRIDGE / ASSET No
NRC-C-2026-014	N/A
REFERENCES	AMENDMENT No
KRU2-MCC-0412-GN-M2D-000001	AMD-0006


SCAN FOR LATEST REV

COPYRIGHT AND DISCLAIMER

This drawing and the related information have been prepared by, or at the request of, Northgate Regional Council for a specific purpose and may not be used for any purpose other than the purpose intended. Northgate Regional Council does not provide any warranties and accepts no liability arising out of the use of this drawing for any other purpose. This drawing is protected by copyright and no part may be reproduced in any form without the express written permission of Northgate Regional Council.

DRAWING COLOUR CODED - PRINT ALL COPIES IN COLOUR

FILE NAME	PLOT DATE & TIME
KRU2-MCC-0412-RW-DRG-000303.dwg	30/10/2026 4:12:05 PM

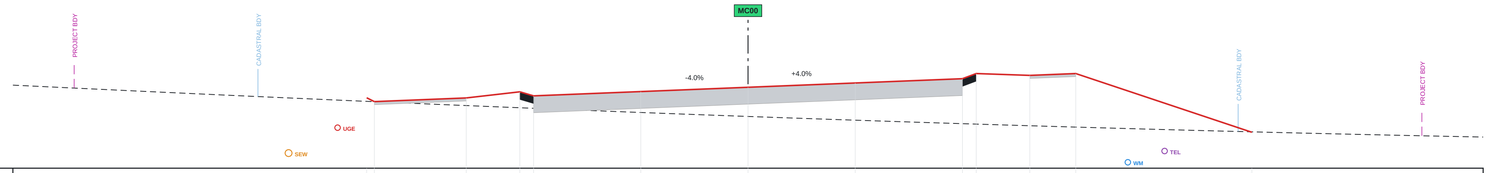


DATUM 8.0

	DAYLIGHT	PATH-OUT	PATH-IN	BOK	KERB	LANE	CL	LANE	KERB	BOK	PATH-IN	PATH-OUT	DAYLIGHT
DESIGN STRINGS													
DESIGN LEVELS	10.298	10.173	10.283	10.493	10.361	10.501	10.641	10.781	10.921	11.089	11.029	11.089	9.172
EXISTING LEVELS	10.161	10.170	10.044	9.972	9.954	9.818	9.688	9.566	9.453	9.439	9.385	9.341	9.186
DESIGN OFFSETS	-12.450	-12.200	-9.200	-7.450	-7.000	-3.500	0.000	3.500	7.000	7.450	9.200	10.700	16.450

CHAINAGE 600

SCALE 1:100

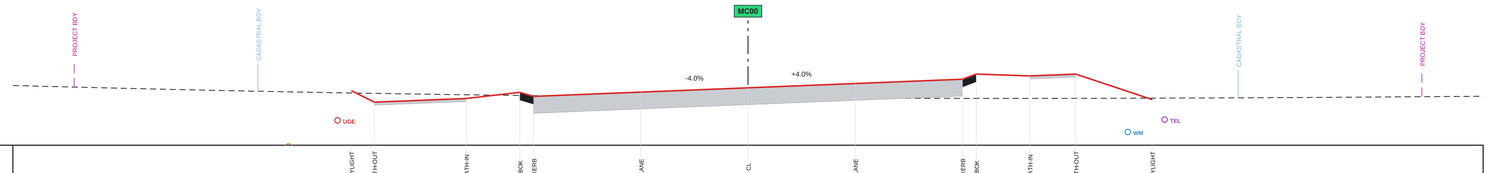


DATUM 9.0

	DAYLIGHT	PATH-OUT	PATH-IN	BOK	KERB	LANE	CL	LANE	KERB	BOK	PATH-IN	PATH-OUT	DAYLIGHT
DESIGN STRINGS													
DESIGN LEVELS	10.780	10.405	10.525	10.725	10.593	10.733	10.873	11.013	11.153	11.321	11.261	11.321	10.488
EXISTING LEVELS	10.704	10.681	10.646	10.623	10.617	10.580	10.564	10.537	10.529	10.529	10.528	10.530	10.536
DESIGN OFFSETS	-12.950	-12.200	-9.200	-7.450	-7.000	-3.500	0.000	3.500	7.000	7.450	9.200	10.700	13.200

CHAINAGE 650

SCALE 1:100

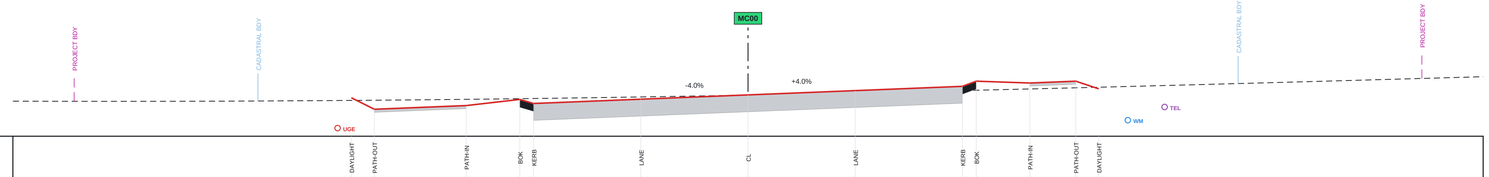


DATUM 11.0

	DAYLIGHT	PATH-OUT	PATH-IN	BOK	KERB	LANE	CL	LANE	KERB	BOK	PATH-IN	PATH-OUT	DAYLIGHT
DESIGN STRINGS													
DESIGN LEVELS	12.255	11.880	12.000	12.200	12.068	12.208	12.348	12.488	12.628	12.796	12.736	12.796	12.546
EXISTING LEVELS	12.168	12.174	12.204	12.225	12.231	12.282	12.343	12.413	12.460	12.501	12.543	12.580	12.599
DESIGN OFFSETS	-12.950	-12.200	-9.200	-7.450	-7.000	-3.500	0.000	3.500	7.000	7.450	9.200	10.700	11.450

CHAINAGE 700

SCALE 1:100

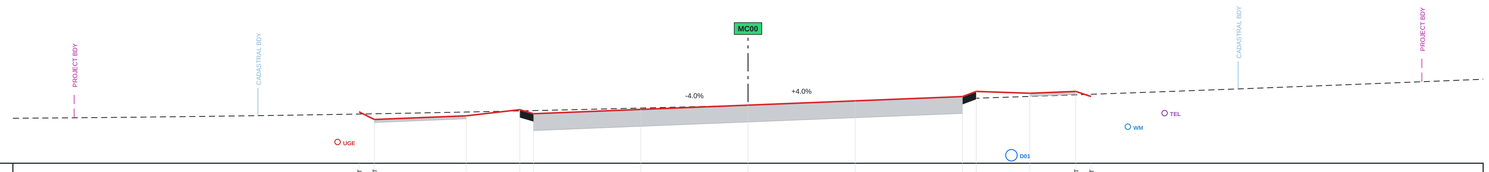

DATUM 12.0

	DAYLIGHT	PATH-OUT	PATH-IN	BOK	KERB	LANE	CL	LANE	KERB	BOK	PATH-IN	PATH-OUT	DAYLIGHT
DESIGN STRINGS													
DESIGN LEVELS	13.678	13.428	13.548	13.748	13.616	13.756	13.896	14.036	14.176	14.344	14.284	14.344	14.177
EXISTING LEVELS	13.606	13.614	13.671	13.708	13.718	13.601	13.894	13.996	14.107	14.122	14.181	14.233	14.250
DESIGN OFFSETS	-12.700	-12.200	-9.200	-7.450	-7.000	-3.500	0.000	3.500	7.000	7.450	9.200	10.700	11.200

CHAINAGE 750

SCALE 1:100

LEGEND

- EXISTING SURFACE
- DESIGN SURFACE
- NEW PAVEMENT
- KERB AND GUTTER
- PROPOSED DRAINAGE (D01)
- EXISTING SEWER (SEW)
- EXISTING WATER MAIN (WM)
- EXISTING UNDERGROUND POWER (UGE)
- EXISTING TELECOMMUNICATIONS (TEL)
- CADASTRAL BOUNDARY
- PROJECT BOUNDARY

NOTES


1. FOR ROADWORKS ALIGNMENT CONTROL PLANS REFER TO DRAWINGS RW-DRG-000031 TO 000034.
2. SECTIONS ARE VIEWED LOOKING UP CHAINAGE. LEFT IS ON THE LEFT.
3. LEVELS ARE IN METRES AHD71. OFFSETS ARE FROM CONTROL LINE MC00.

0 2 4 8m

SCALE 1:100 @A1

KEY PLAN

NOT TO SCALE

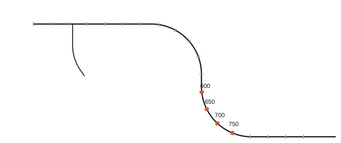

CLIENT

NORTHGATE REGIONAL COUNCIL
Infrastructure Delivery | Roads & Drainage

PROJECT

PROJECT No 25-0412

KESTREL ROAD UPGRADE

STAGE 2

Marlow Street to Ironbark Avenue
Northgate NSW 2217

DESIGN PACKAGE RW01 | ROADWORKS

PREPARED BY

MERIDIAN
CIVIL CONSULTING

Level 9, 140 Harbour Street, Sydney NSW 2000
Tel: +61 2 5550 0142
meridiancivil.example

DRAWING TITLE

CROSS SECTIONS

CONTROL LINE MC00 CH 600-750

SHEET 4 OF 5

DRAWING No.

KRU2-MCC-0412-RW-DRG-000304

REV	STATUS / SUITABILITY	ISSUE DATE
C	S3 FOR REVIEW AND COMMENT Not for construction	30.10.26

EDMS No	SHEET SIZE	SCALE @ A1
DS2026/01877	A1	1:100

REV	DESCRIPTION	BY	CHK	APP	DATE
A	50% DETAILED DESIGN	AN	SI	TM	28.05.26
B	80% DETAILED DESIGN	AN	SI	TM	14.08.26
C	100% DETAILED DESIGN	AN	SI	TM	30.10.26

ROLE	NAME	INITIALS	DATE
DRAWN	AMINA NGUYEN	AN	30.10.26
DESIGNED	RAFAEL OKAFOR	RO	30.10.26
DRAWING CHECK	LENA HARTMANN	LH	30.10.26
DESIGN CHECK	SANJAY IYER	SI	30.10.26
PROJECT MANAGER	DEIRDRE KOWALSKI	DK	30.10.26
APPROVED	TOBY McALLISTER	TM	30.10.26

COORDINATE SYSTEM	HEIGHT DATUM
GDA2020 / MGA ZONE 56	AHD71
DISCIPLINE	DESIGN LOT CODE
ROADWORKS	LOT-03
CONTRACT No	BRIDGE / ASSET No
NRC-C-2026-014	N/A
REFERENCES	AMENDMENT No
KRU2-MCC-0412-GN-M2D-000001	AMD-0006

SCAN FOR LATEST REV

COPYRIGHT AND DISCLAIMER
This drawing and the related information have been prepared by, or at the request of, Northgate Regional Council for a specific purpose and may not be used for any purpose other than the purpose intended. Northgate Regional Council does not provide any warranties and accepts no liability arising out of the use of this drawing for any other purpose. This drawing is protected by copyright and no part may be reproduced in any form without the express written permission of Northgate Regional Council.

DRAWING COLOUR CODED - PRINT ALL COPIES IN COLOUR

FILE NAME	PLOT DATE & TIME
KRU2-MCC-0412-RW-DRG-000304.dwg	30/10/2026 4:12:05 PM


PROJECT BDY
CADASTRAL BDY
MC00
-3.8%
+2.6%
CADASTRAL BDY
PROJECT BDY
UGE
TEL
WM
D03

DATUM 13.0

| | | |